

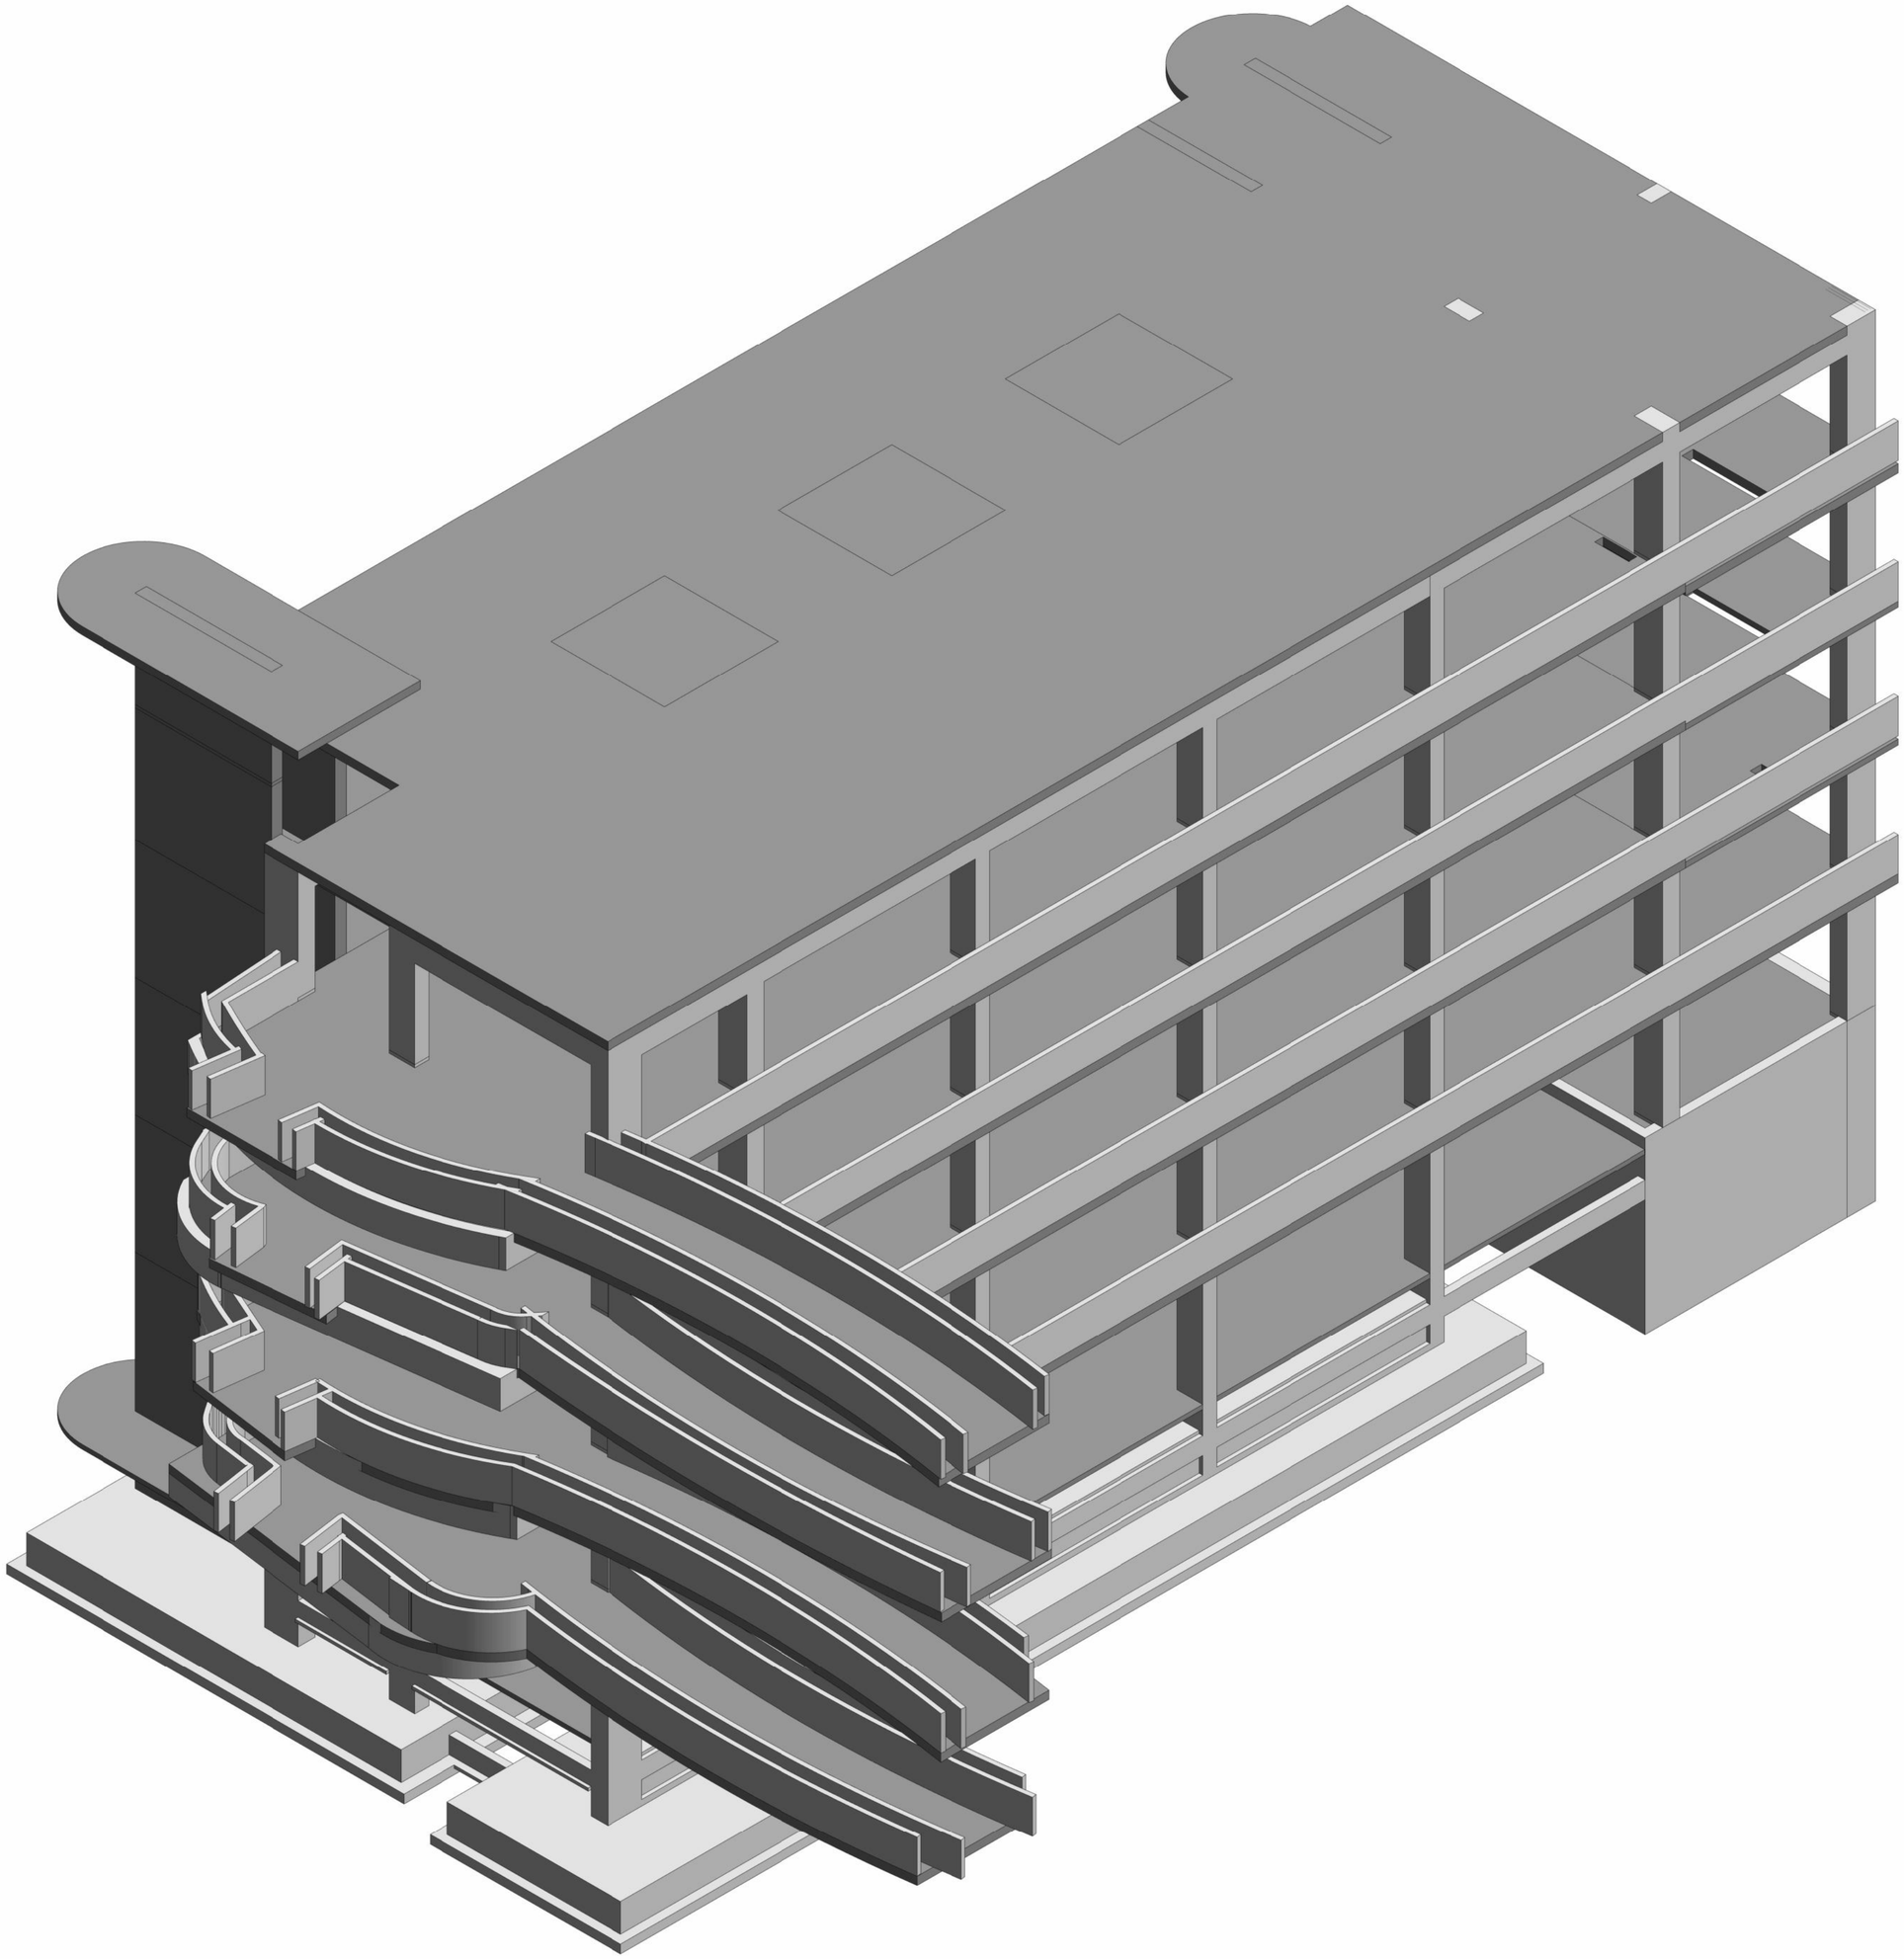


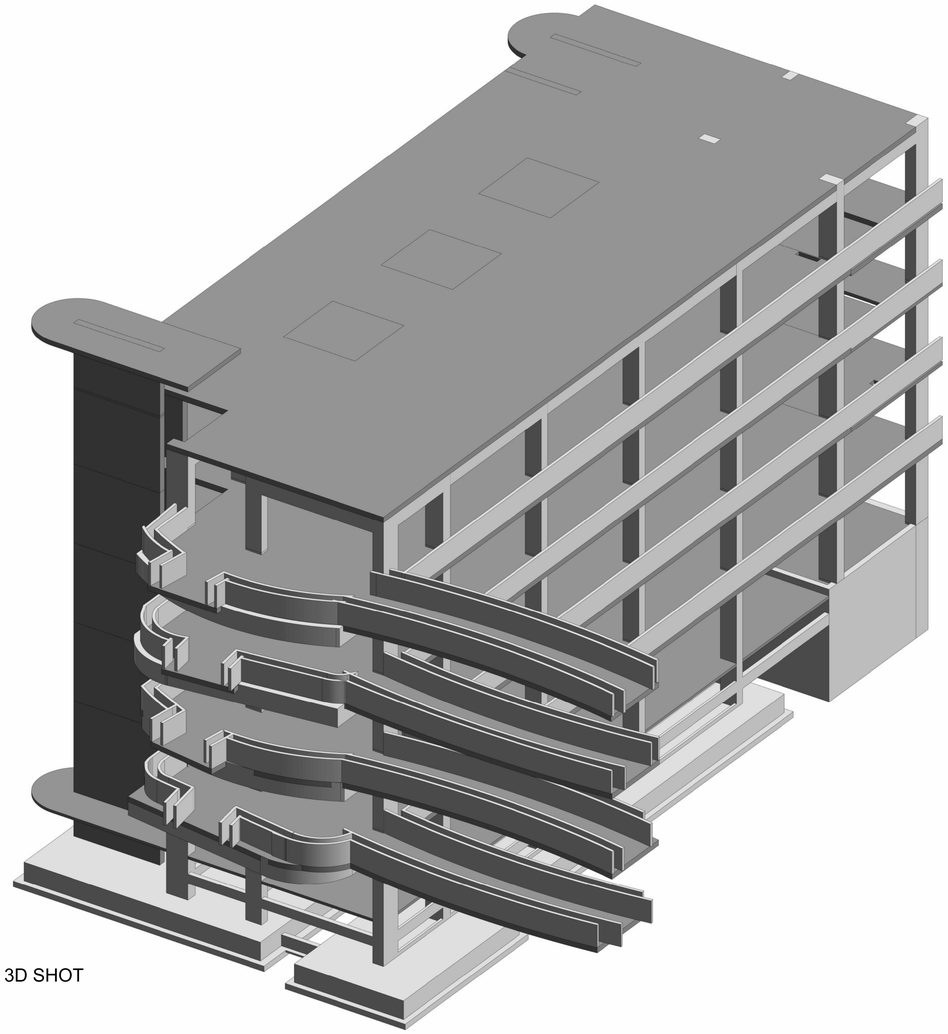


1 3D SHOT

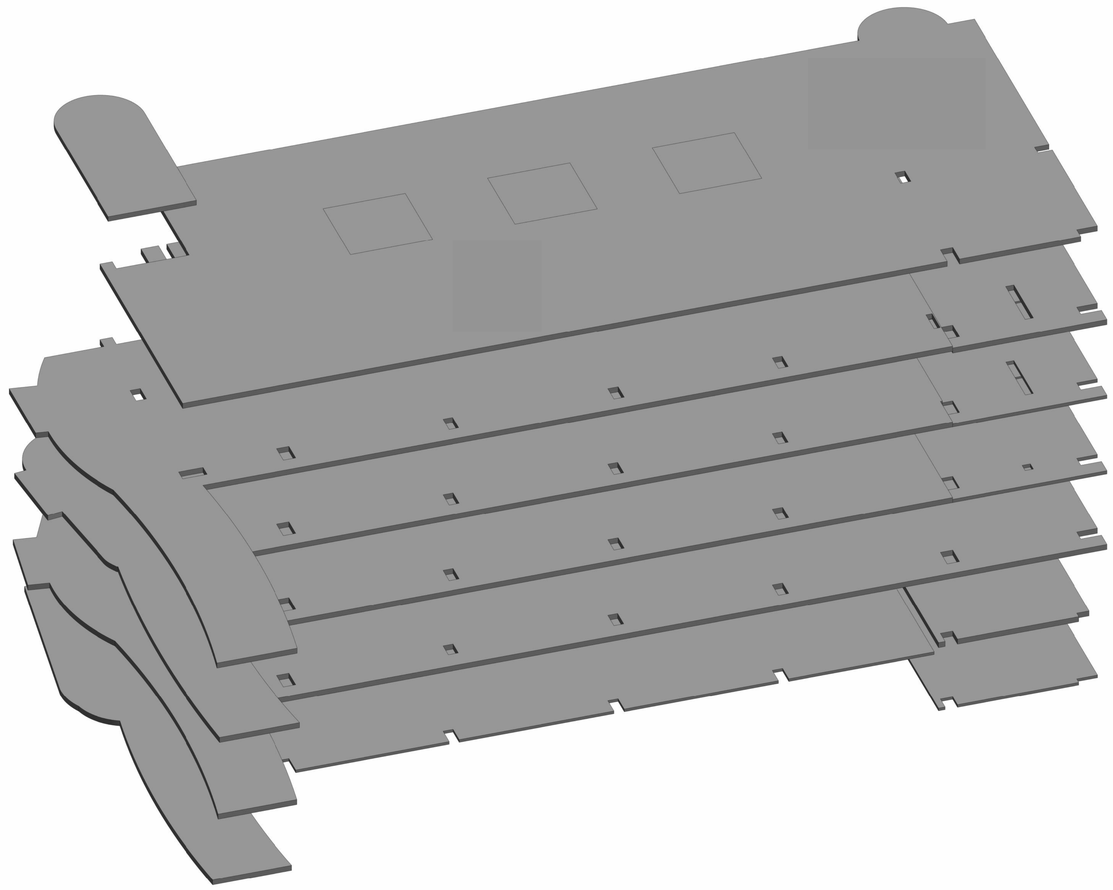

2 3D SHOT FLOORS

Sheet List	
Sheet Name	Sheet Number
Cover Sheet	A100
FOUNDATION LAYOUT PLAN-Concrete Dimention&Sec	A101
COULMN & AXIS	A102
GROUND FLOOR-Concrete Dimention&Sec	A103
FIRST FLOOR-Concrete Dimention&Sec	A104
TYPICAL FLOOR-Concrete Dimention&Sec	A105
Q.S-Concrete	A106
Lower Roof Floor-Concrete Dimention&Sec	A107
RFT DETAILING FOR B1&B2	A108
RFT DETAILING FOR F4 (SHEET1)	A109
RFT DETAILING FOR F4 (SHEET2)	A110
RFT DETAILING FOR F4 (SHEET3)	A111
RFT DETAILING FOR F4 (SHEET4)	A112
RFT DETAILING FOR W1	A113
RFT DETAILING FOR W4	A114
RFT DETAILING FOR C5	A115
BBS Sheet - Coulmns&Beams	A116
BBS Sheet-Foundation-1	A117
BBS Sheet-Foundation-2	A118
BBS Sheet-Foundation-3	A119

KEY PLAN

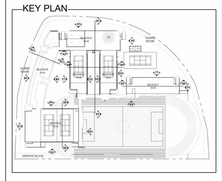

LEGEND

No.	Description	Date

Client Name:

Project Name:

school 1

Cover Sheet

Project number

Date **Issue Date**


Drawn by **KHALID ATEF**

Checked by **Checker**


Drawing No. **S-A100-**

Scale

01/11/2026 09:07:38 ص

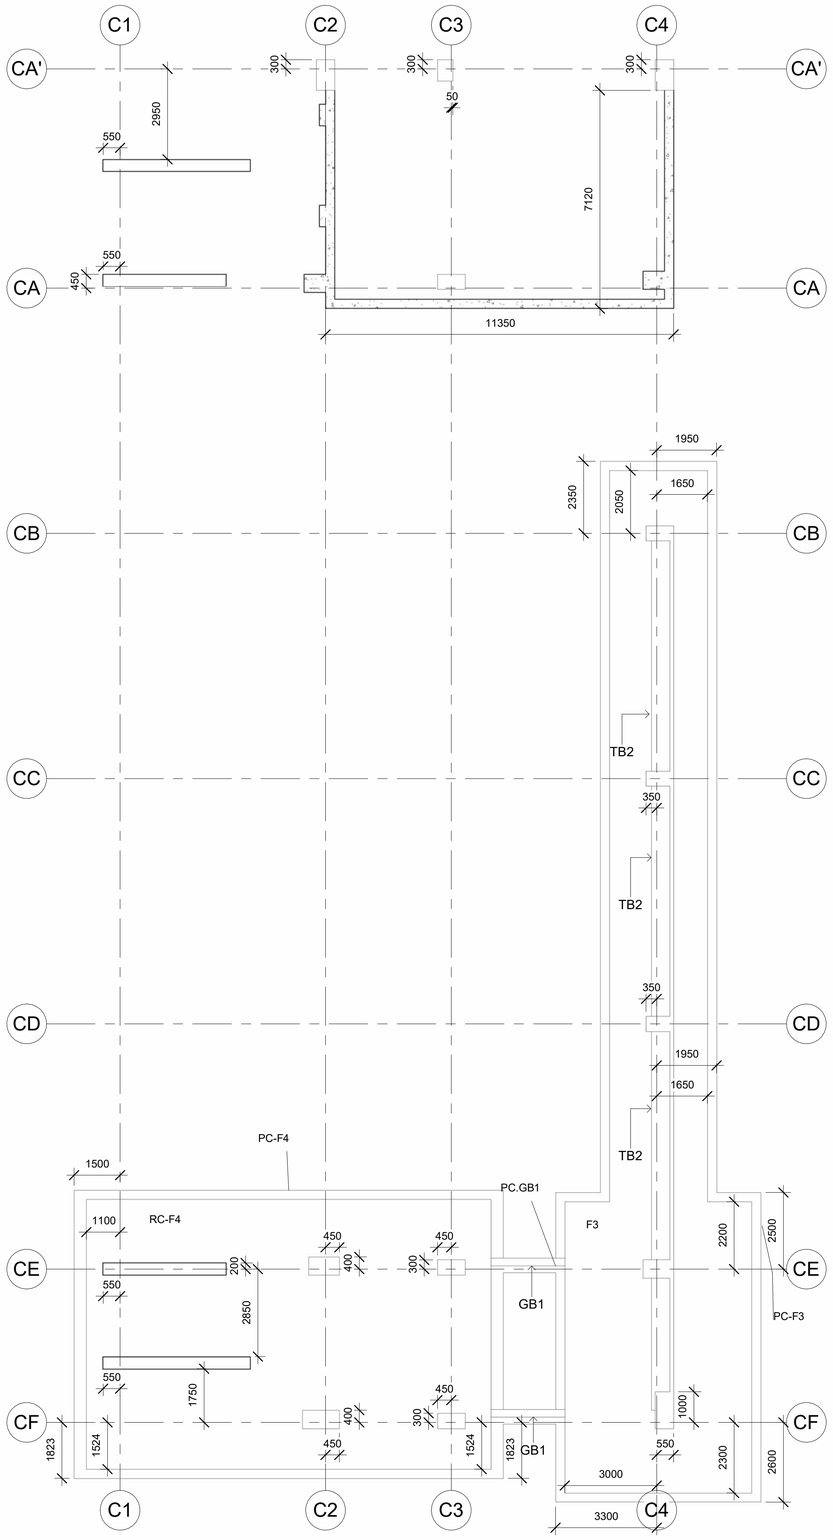


00-FOUNDATION Basement
02 PLAN
1 : 100

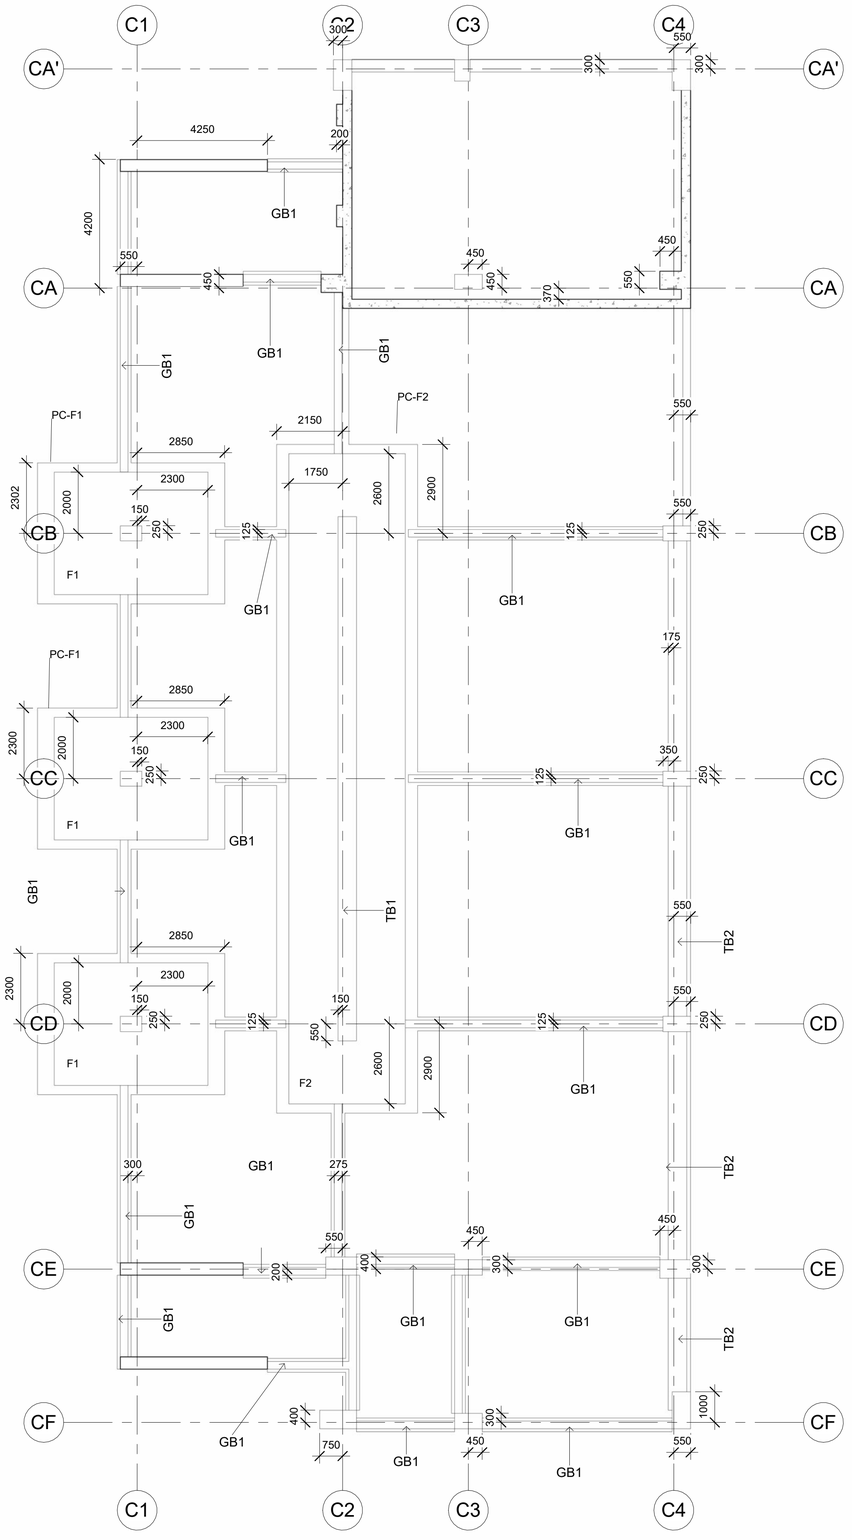

01-FOUNDATION Basement
01 PLAN
1 : 100

KEY PLAN

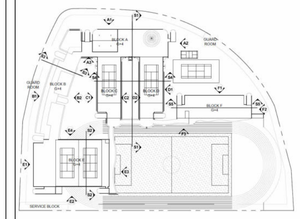


No.	Description	Date
00	Revision 1	Date 1

school 1

FOUNDATION LAYOUT PLAN-Concrete Dimention&Sec

Project number	
Date	Issue Date
Drawn by	KHALID ATEF
Checked by	Checker
A101	
Scale	1 : 100


01/11/2026 09:07:50 ص

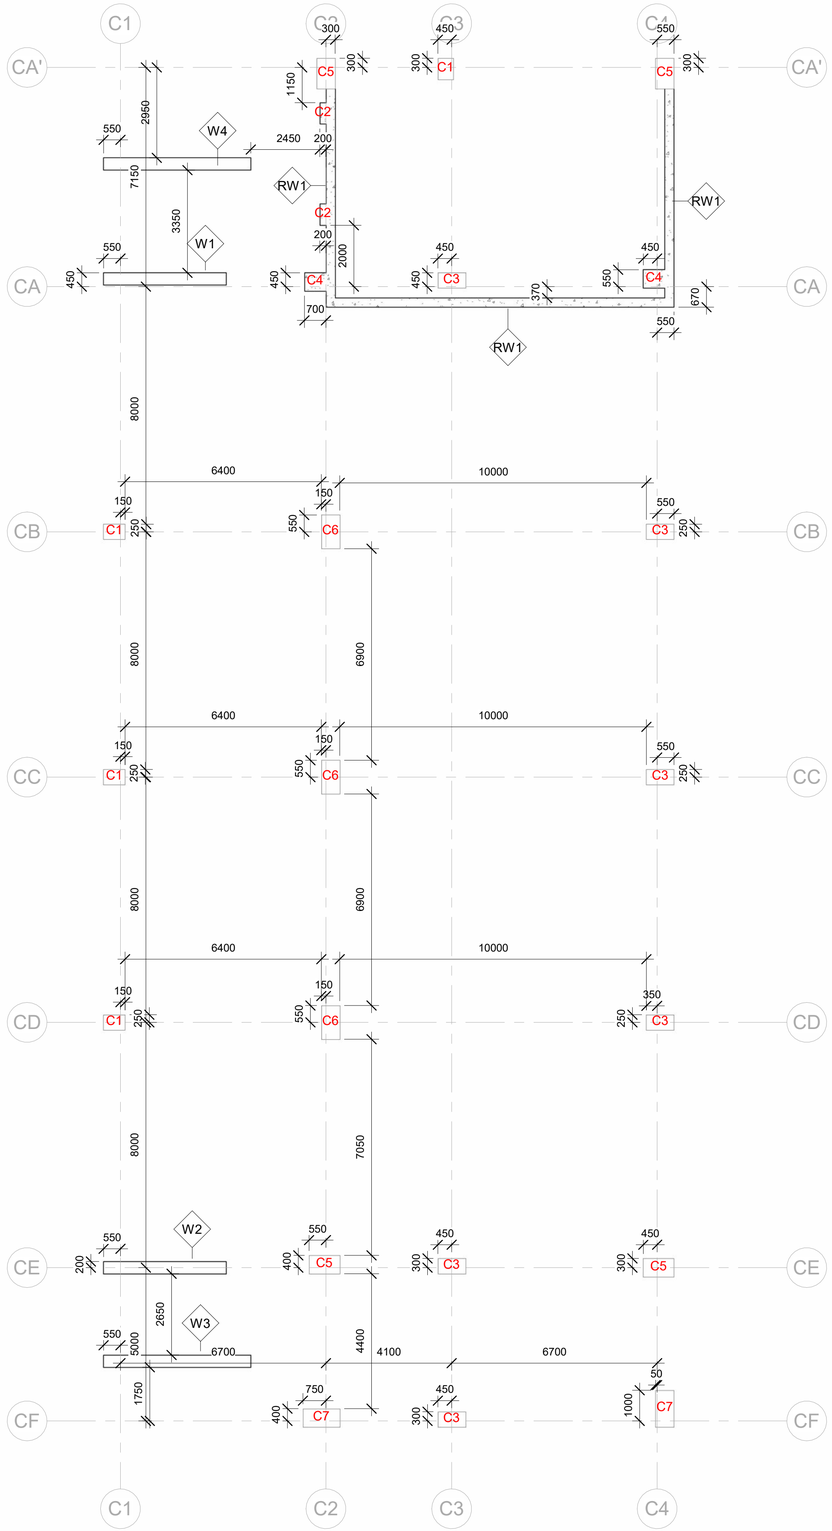

1 02-COULMNS AXIS

1 : 100

KEY PLAN

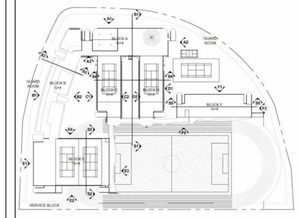

No.	Description	Date
00	Revision 1	Date 1

school 1

COULMN & AXIS

Project number

Date Issue Date


Drawn by KHALID ATEF

Checked by Checker

A102


Scale 1 : 100

01/11/2026 09:08:01 ص

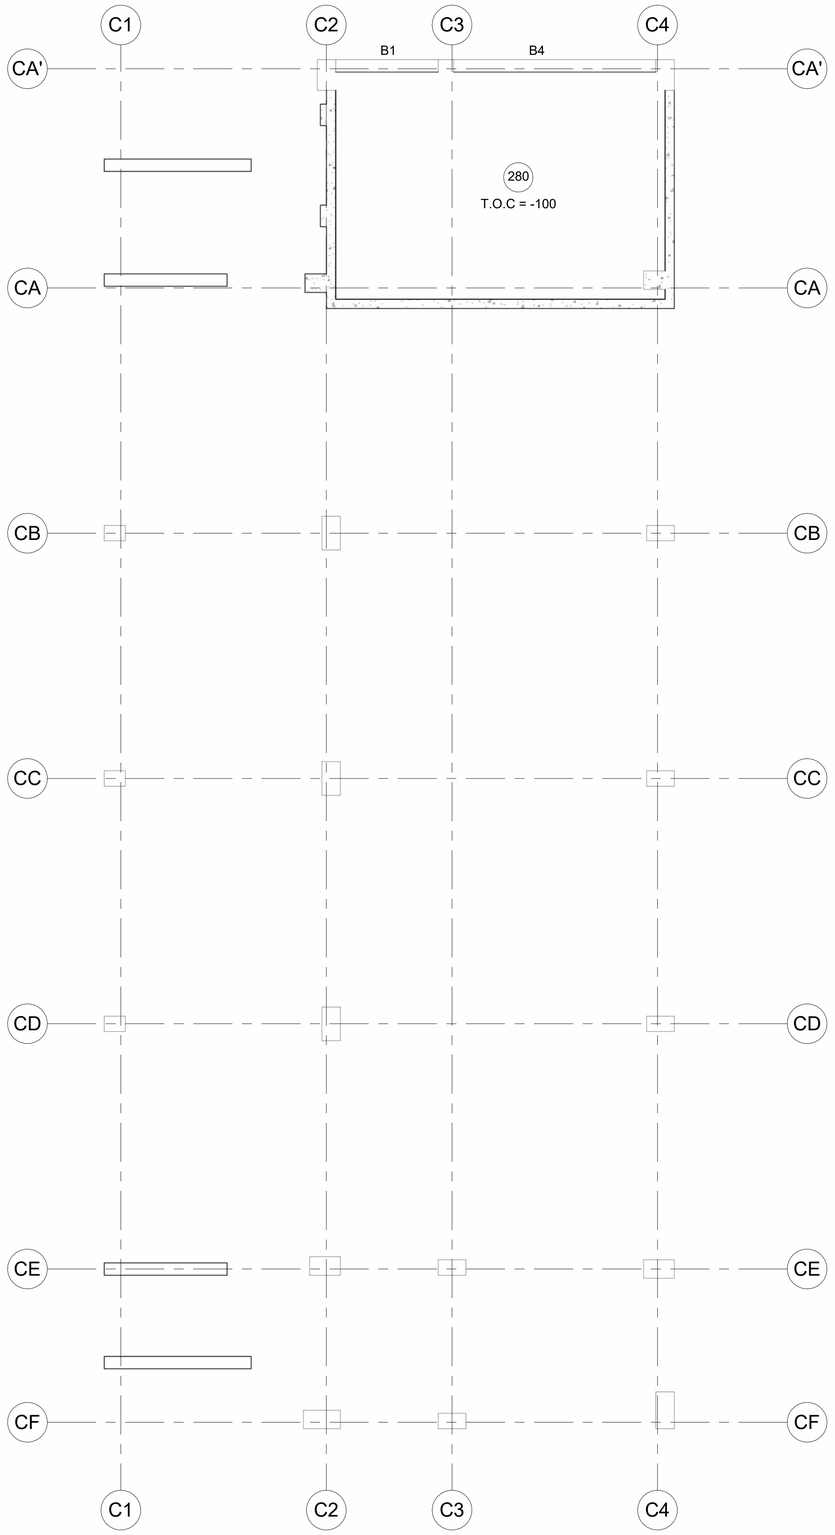

1 02-Ground Floor
1 : 100

KEY PLAN

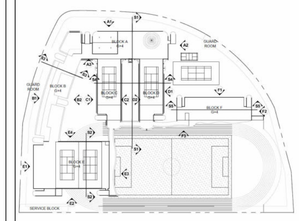


No.	Description	Date
00	Revision 1	Date 1

school 1


GROUND FLOOR-Concrete Dimention&Sec

Project number	
Date	Issue Date
Drawn by	KHALID ATEF
Checked by	Checker
A103	
Scale	1 : 100


01/11/2026 09:08:13 ص

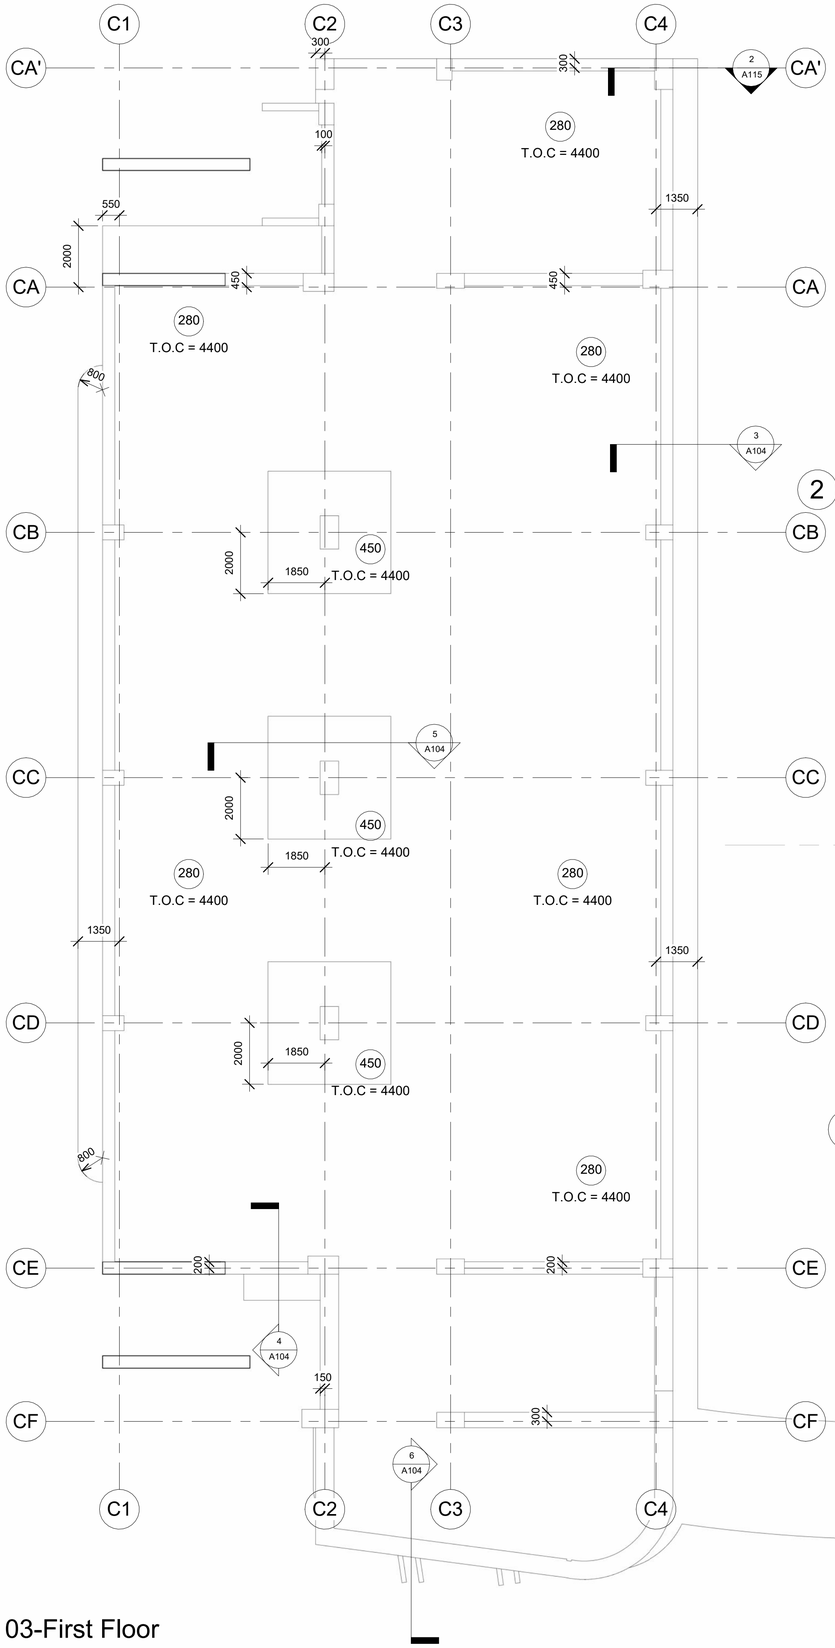


1 03-First Floor
1 : 100

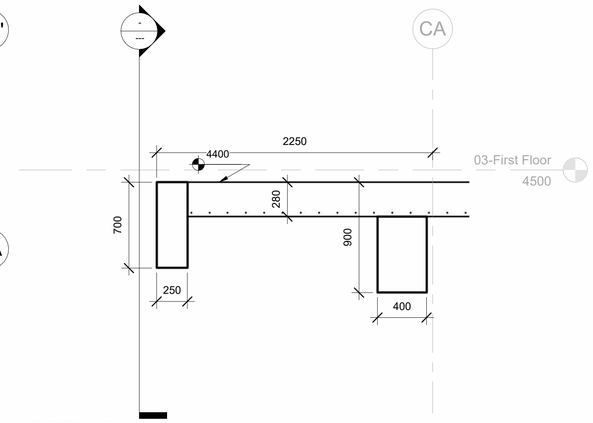


2 DETAIL Section 1
1 : 25

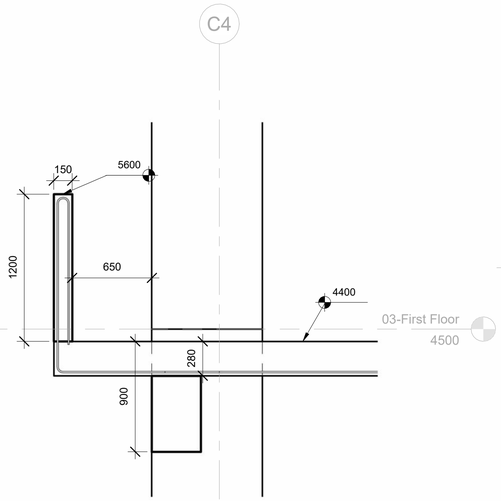


3 DETAIL Section 2
1 : 25

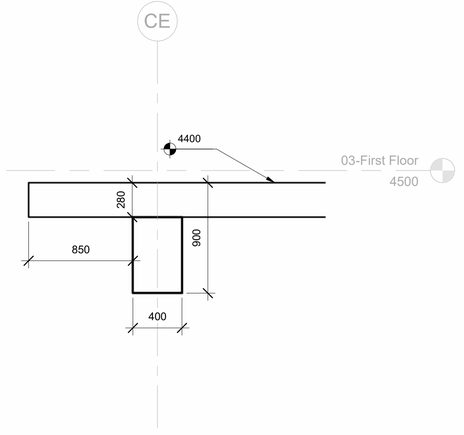

4 DETAIL Section 3
1 : 25

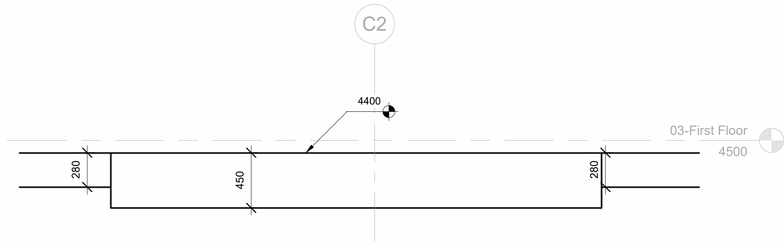


5 DETAIL Section 4
1 : 25

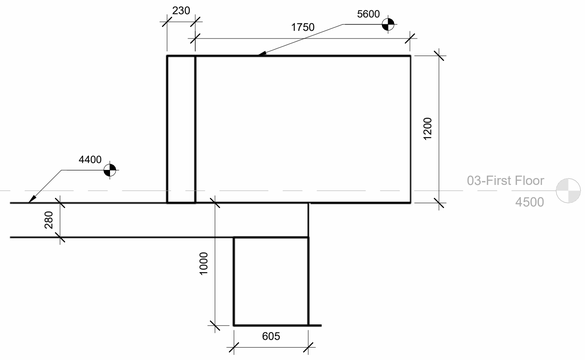

6 DETAIL Section 5
1 : 25

KEY PLAN

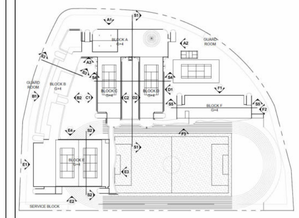


No.	Description	Date
00	Revision 1	Date 1


school 1

FIRST FLOOR-Concrete Dimention&Sec


Project number	
Date	Issue Date
Drawn by	KHALID ATEF
Checked by	Checker
A104	
Scale	As indicated

01/11/2026 09:08:25 ص

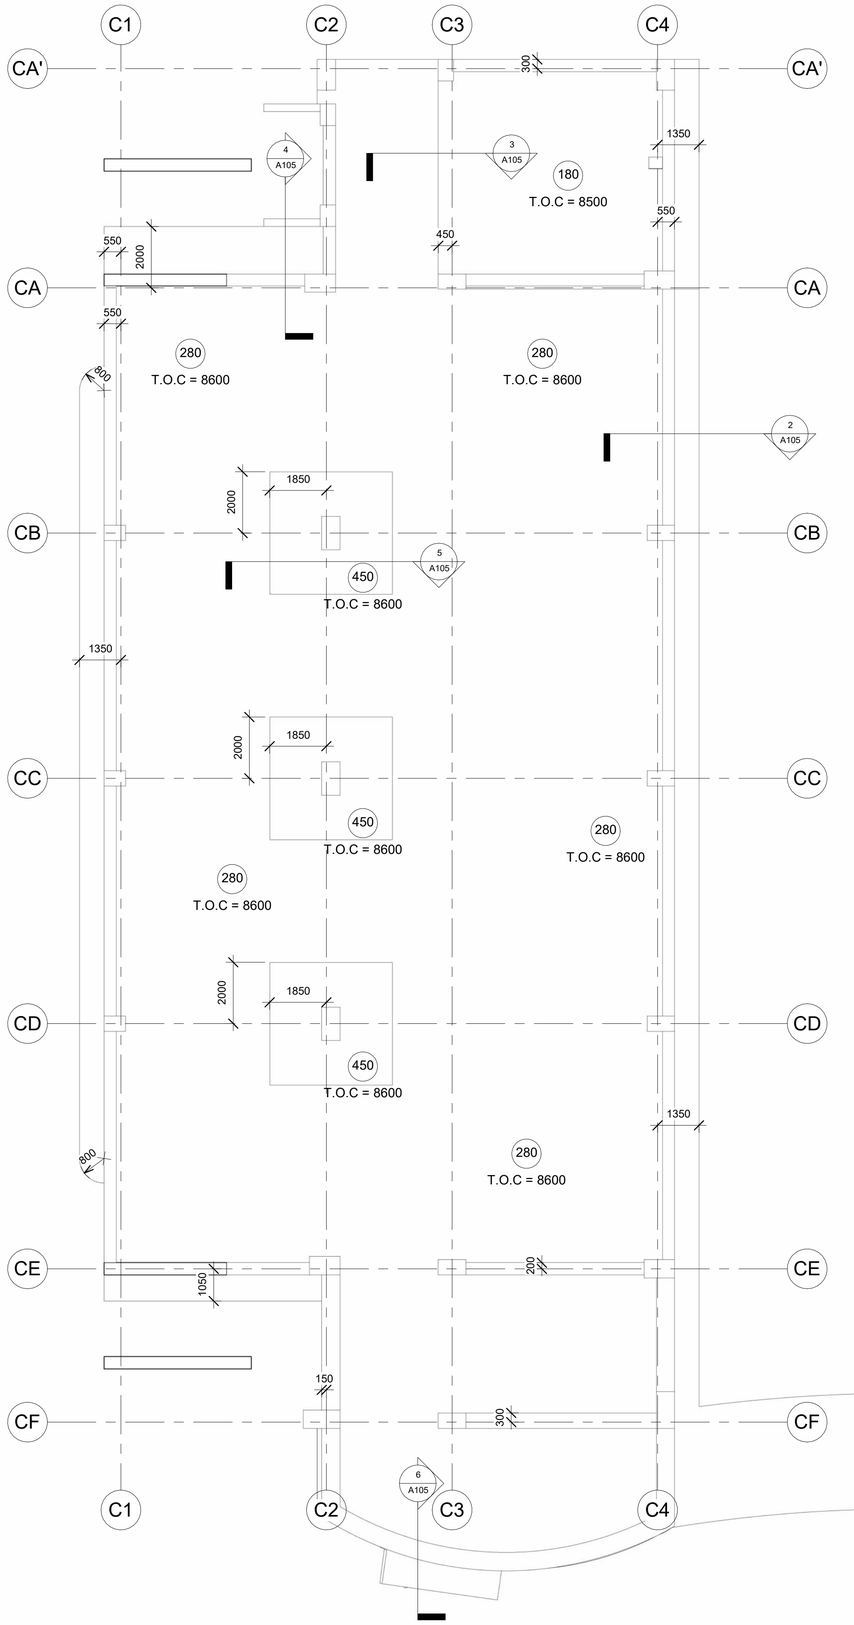


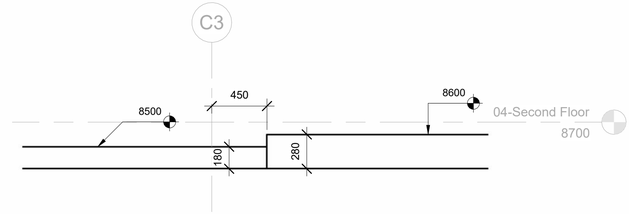


3 DETAIL Section 7
1 : 25

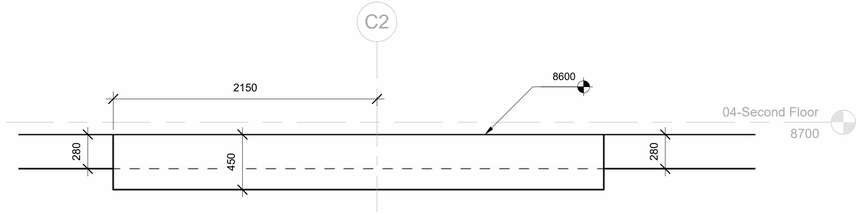


5 DETAIL Section 9
1 : 25

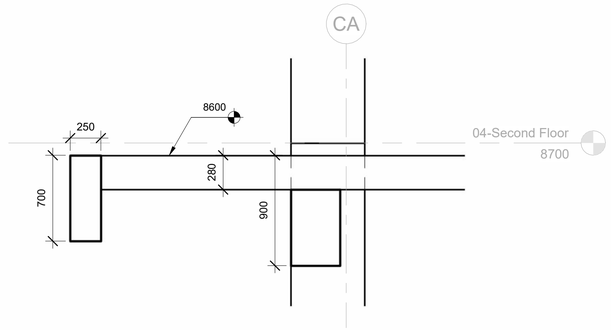

4 DETAIL Section 8
1 : 25

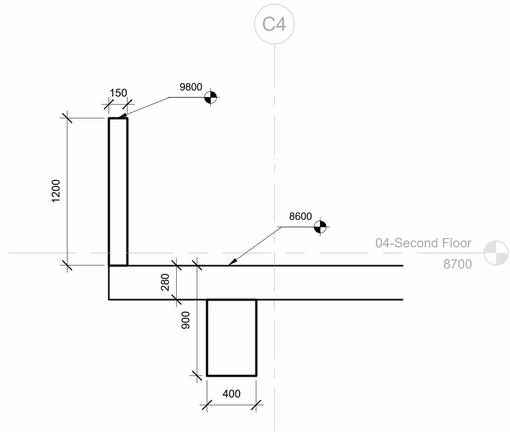


2 DETAIL Section 6
1 : 25

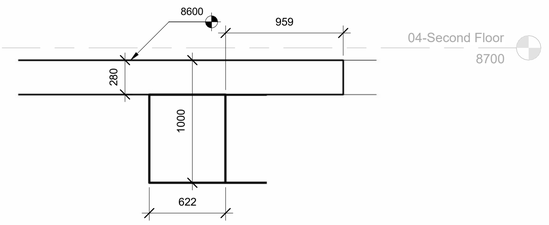

6 DETAIL Section 10
1 : 25

KEY PLAN

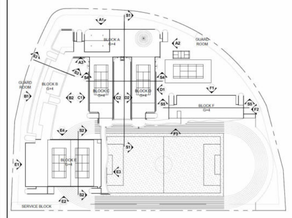

No.	Description	Date
00	Revision 1	Date 1

school 1

TYPICAL FLOOR-Concrete Dimention&Sec

Project number	
Date	Issue Date
Drawn by	KHALID ATEF
Checked by	Checker
A105	
Scale	As indicated

01/11/2026 09:08:38

KT-R14-G07-Structural Columns			
Base Level	Count	Comments	Volume
00-Basement 02 Floor	1	C1	2.10 m³
00-Basement 02 Floor	2	C2	1.68 m³
00-Basement 02 Floor	1	C3	2.70 m³
00-Basement 02 Floor	2	C4	5.04 m³
00-Basement 02 Floor	2	C5	7.20 m³
02-Ground Floor	4	C1	7.25 m³
02-Ground Floor	2	C2	3.05 m³
02-Ground Floor	1	C3	2.03 m³
02-Ground Floor	2	C4	5.40 m³
02-Ground Floor	2	C5	5.40 m³
02-Ground Floor	3	C6	10.69 m³
03-First Floor	5	C1	7.76 m³
03-First Floor	3	C2	4.63 m³
03-First Floor	9	C3	23.74 m³
03-First Floor	2	C4	5.04 m³
03-First Floor	6	C5	18.72 m³
03-First Floor	3	C6	8.32 m³
03-First Floor	4	C7	16.01 m³
04-Second Floor	5	C1	7.77 m³
04-Second Floor	3	C2	4.83 m³
04-Second Floor	4	C3	7.55 m³
04-Second Floor	2	C4	5.04 m³
04-Second Floor	4	C5	10.08 m³
04-Second Floor	3	C6	8.32 m³
04-Second Floor	2	C7	6.05 m³
05-Third Floor	5	C1	7.77 m³
05-Third Floor	3	C2	4.83 m³
05-Third Floor	4	C3	7.55 m³
05-Third Floor	2	C4	5.04 m³
05-Third Floor	4	C5	10.08 m³
05-Third Floor	3	C6	7.43 m³
05-Third Floor	2	C7	5.85 m³
06-Fourth Floor	5	C1	7.17 m³
06-Fourth Floor	3	C2	4.39 m³
06-Fourth Floor	4	C3	7.00 m³
06-Fourth Floor	2	C4	4.75 m³
06-Fourth Floor	4	C5	9.34 m³
06-Fourth Floor	3	C6	7.23 m³
06-Fourth Floor	2	C7	5.50 m³
	123		280.30 m³


KT-R14-G07-Structural Floors				
Level	Count	Area	Core Thickness	Volume
01-Basement 01 Floor	1	83 m²	150	12.39 m³
		83 m²		12.39 m³
02-Ground Floor	1	719 m²	150	107.85 m³
02-Ground Floor	1	79 m²	280	22.00 m³
		798 m²		129.85 m³
03-First Floor	1	862 m²	280	241.43 m³
03-First Floor	1	46 m²	450	20.71 m³
		908 m²		262.14 m³
04-Second Floor	1	62 m²	180	11.08 m³
04-Second Floor	1	806 m²	280	225.70 m³
04-Second Floor	1	46 m²	450	20.71 m³
		914 m²		257.49 m³
05-Third Floor	1	61 m²	180	10.92 m³
05-Third Floor	1	803 m²	280	224.71 m³
05-Third Floor	1	46 m²	450	20.71 m³
		909 m²		256.34 m³
06-Fourth Floor	2	866 m²	280	242.38 m³
06-Fourth Floor	1	48 m²	450	21.60 m³
		914 m²		263.98 m³
07-Lower Roof Floor	1	758 m²	280	212.30 m³
07-Lower Roof Floor	1	48 m²	450	21.60 m³
		806 m²		233.90 m³
08-Upper Roof Floor	1	40 m²	260	10.38 m³
		40 m²		10.38 m³
17		5371 m²		1426.48 m³

KT-R14-G07-Structural Foundation			
Level	Comments	Count	Volume
00-Basement 02 Floor	F3	1	134.27 m³
00-Basement 02 Floor	PC-F3	1	47.49 m³
00-Basement 02 Floor	PC-F4	1	39.47 m³
00-Basement 02 Floor	RC-F4	1	116.16 m³
			337.39 m³
01-Basement 01 Floor	F1	3	54.00 m³
01-Basement 01 Floor	F2	1	72.50 m³
01-Basement 01 Floor	PC-F1	1	25.25 m³
01-Basement 01 Floor	PC-F2	1	30.08 m³
01-Basement 01 Floor	PC.GB1	6	4.70 m³
			186.55 m³
Grand total: 16			523.94 m³

KT-R14-G07-Structural Framing			
Reference Level	Comments	Count	Volume
01-Basement 01 Floor	GB1	31	16.96 m³
01-Basement 01 Floor	TB1	2	0.83 m³
01-Basement 01 Floor	TB2	8	24.30 m³
02-Ground Floor	B1	1	1.21 m³
02-Ground Floor	B4	1	2.38 m³
03-First Floor	B1	5	14.47 m³
03-First Floor	B2	2	1.30 m³
03-First Floor	B3	1	1.44 m³
03-First Floor	B4	1	1.44 m³
03-First Floor	B5	1	2.23 m³
03-First Floor	B7	1	1.87 m³
03-First Floor	B8	2	3.72 m³
03-First Floor	B9	1	1.93 m³
03-First Floor	B10	1	1.66 m³
03-First Floor	B11	1	1.90 m³
03-First Floor	B13	1	1.09 m³
03-First Floor	B14	1	1.60 m³
03-First Floor	B15	4	7.48 m³
03-First Floor	B16	1	1.46 m³
03-First Floor	B17	2	4.92 m³
03-First Floor	B19	4	5.77 m³
03-First Floor	B20	1	0.38 m³
03-First Floor	B21	1	0.64 m³
03-First Floor	PARAPET	21	10.73 m³
04-Second Floor	B1	5	14.72 m³
04-Second Floor	B2	2	1.30 m³
04-Second Floor	B3	1	1.67 m³
04-Second Floor	B4	1	1.44 m³
04-Second Floor	B5	1	2.23 m³
04-Second Floor	B7	1	1.87 m³
04-Second Floor	B8	2	3.72 m³
04-Second Floor	B9	1	1.93 m³
04-Second Floor	B10	1	1.33 m³
04-Second Floor	B11	1	1.90 m³
04-Second Floor	B13	1	1.45 m³
04-Second Floor	B14	1	1.60 m³
04-Second Floor	B15	4	7.48 m³
04-Second Floor	B16	1	1.70 m³
04-Second Floor	B18	2	5.17 m³
04-Second Floor	B19	3	5.31 m³
04-Second Floor	B20	1	0.38 m³
04-Second Floor	B21	1	0.64 m³
04-Second Floor	PARAPET	12	10.53 m³
05-Third Floor	B1	1	1.90 m³
05-Third Floor	B2	2	1.30 m³
05-Third Floor	B3	1	1.67 m³

KT-R14-G07-Structural Framing			
Reference Level	Comments	Count	Volume
05-Third Floor	B4	1	1.44 m³
05-Third Floor	B5	1	2.23 m³
05-Third Floor	B7	1	1.87 m³
05-Third Floor	B8	2	3.72 m³
05-Third Floor	B9	1	1.93 m³
05-Third Floor	B10	1	1.73 m³
05-Third Floor	B11	1	1.90 m³
05-Third Floor	B13	1	1.73 m³
05-Third Floor	B14	1	1.60 m³
05-Third Floor	B15	4	7.48 m³
05-Third Floor	B16	1	1.70 m³
05-Third Floor	B19	4	5.92 m³
05-Third Floor	B20	1	0.38 m³
05-Third Floor	B21	1	0.64 m³
05-Third Floor	PARAPET	20	28.05 m³
06-Fourth Floor	B1	1	1.64 m³
06-Fourth Floor	B2	2	1.30 m³
06-Fourth Floor	B3	1	1.44 m³
06-Fourth Floor	B4	1	1.44 m³
06-Fourth Floor	B5	1	2.23 m³
06-Fourth Floor	B7	1	1.87 m³
06-Fourth Floor	B8	2	3.72 m³
06-Fourth Floor	B9	1	1.93 m³
06-Fourth Floor	B10	1	1.62 m³
06-Fourth Floor	B11	1	1.90 m³
06-Fourth Floor	B13	1	1.67 m³
06-Fourth Floor	B14	1	1.60 m³
06-Fourth Floor	B15	4	7.48 m³
06-Fourth Floor	B16	1	1.46 m³
06-Fourth Floor	B19	3	5.94 m³
06-Fourth Floor	B20	1	0.38 m³
06-Fourth Floor	B21	1	0.64 m³
06-Fourth Floor	PARAPET	18	28.84 m³
07-Lower Roof Floor	B1	2	3.26 m³
07-Lower Roof Floor	B2	1	0.67 m³
07-Lower Roof Floor	B3	3	2.39 m³
07-Lower Roof Floor	B4	1	1.44 m³
07-Lower Roof Floor	B5	1	2.23 m³
07-Lower Roof Floor	B7	3	5.65 m³
07-Lower Roof Floor	B8	2	2.70 m³
07-Lower Roof Floor	B9	1	0.81 m³
07-Lower Roof Floor	B11	1	1.90 m³
07-Lower Roof Floor	B13	5	9.08 m³
07-Lower Roof Floor	B14	1	1.46 m³
07-Lower Roof Floor	B15	2	0.48 m³
07-Lower Roof Floor	B16	1	0.64 m³
Grand total: 248		248	345.14 m³

KEY PLAN

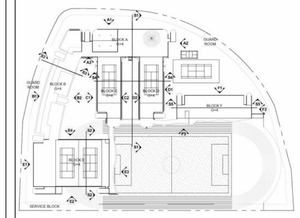

No.	Description	Date
00	Revision 1	Date 1

school 1

Q.S-Concrete

Project number

Date Issue Date


Drawn by KHALID ATEF

Checked by Checker


A106

Scale


01/11/2026 09:08:49 ص

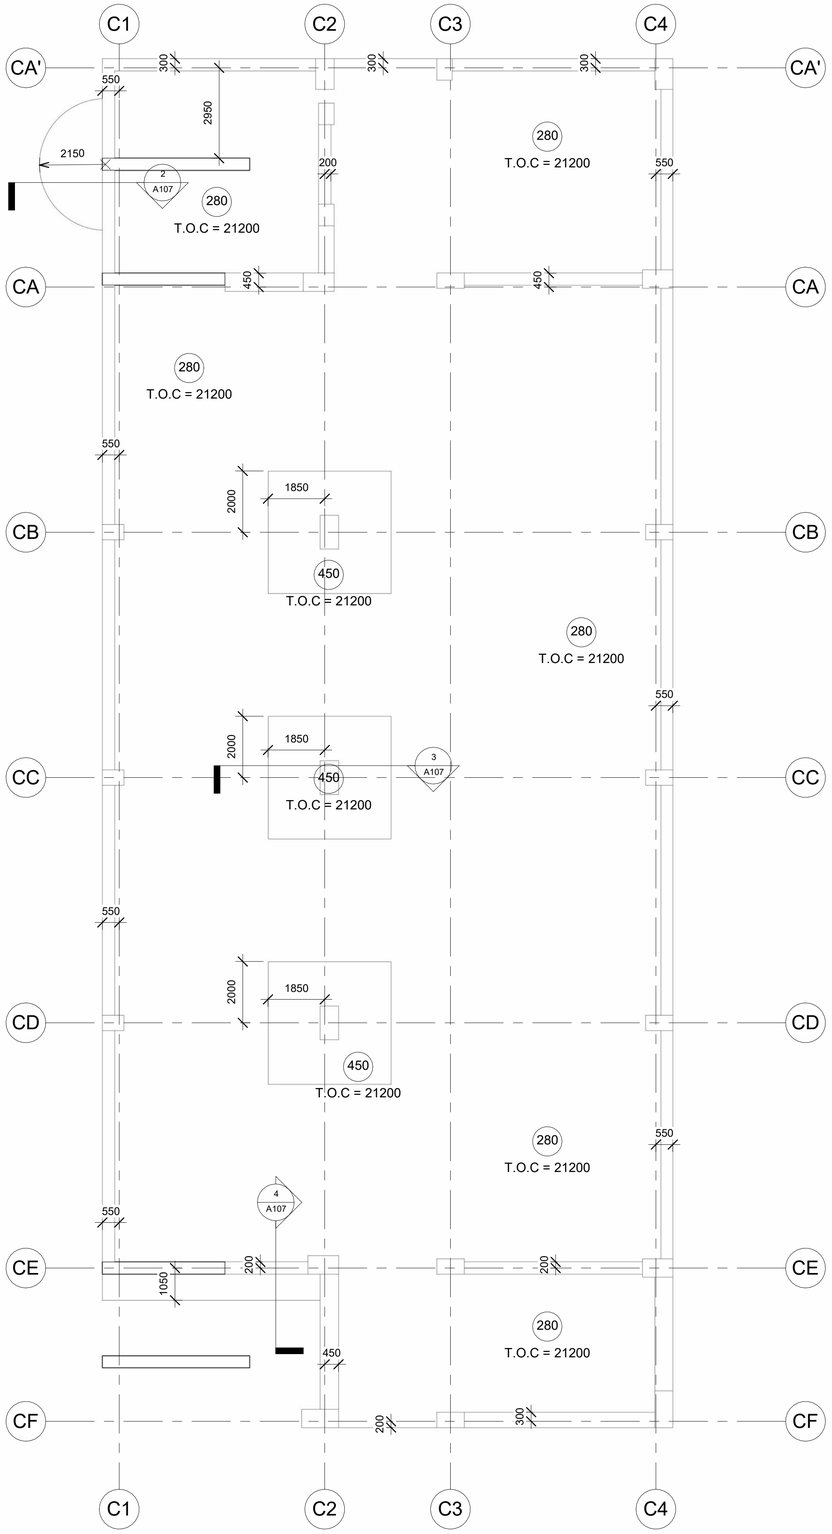


1 07-Lower Roof Floor
1 : 100

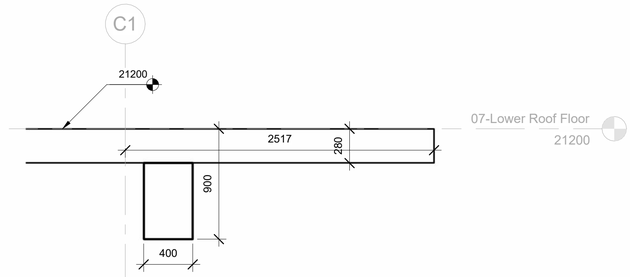

2 DETAIL Section 16
1 : 25

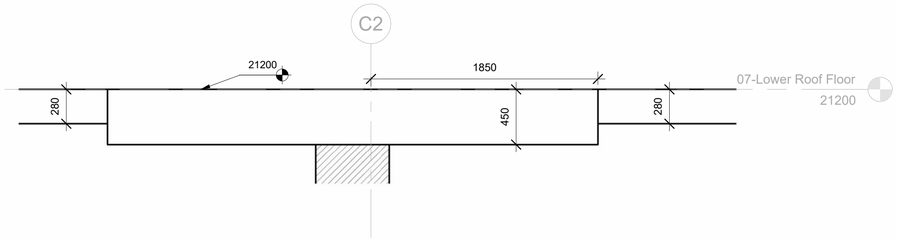


3 DETAIL Section 17
1 : 25

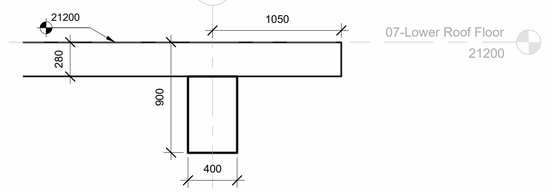

4 DETAIL Section 18
1 : 25

KEY PLAN

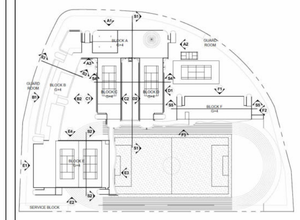


No.	Description	Date
00	Revision 1	Date 1

school 1

Lower Roof Floor-Concrete Dimention&Sec


Project number	
Date	Issue Date
Drawn by	KHALID ATEF
Checked by	Checker
A107	
Scale	As indicated

01/11/2026 09:09:02 ص

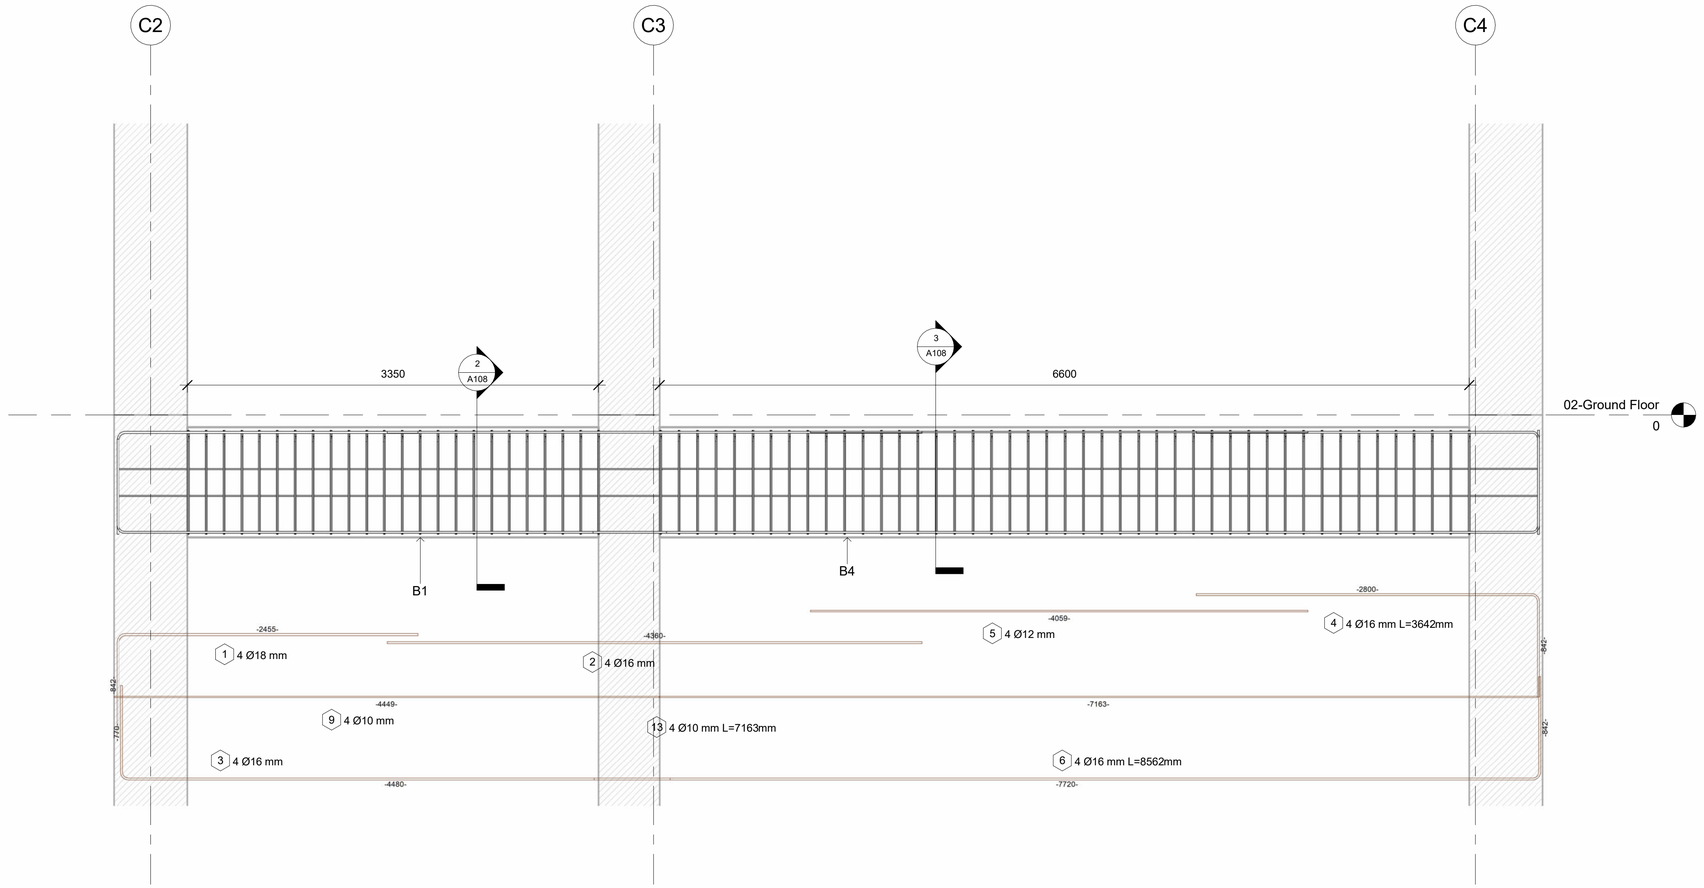


1 SEC B1&B4 RFT

1 : 25

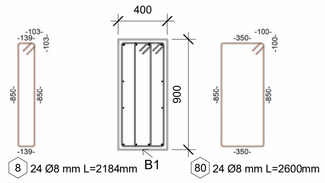

2 CROSS SEC B1 RFT1


1 : 25

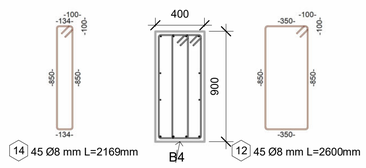

3 CROSS SEC B4 RFT1

1 : 25

KEY PLAN

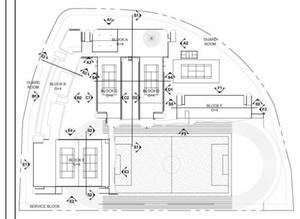


No.	Description	Date

school 1

RFT DETAILING FOR B1&B2


Project number	
Date	Issue Date
Drawn by	khalid atef
Checked by	Checker
A108	
Scale	1 : 25

01/11/2026 09:09:14 ص

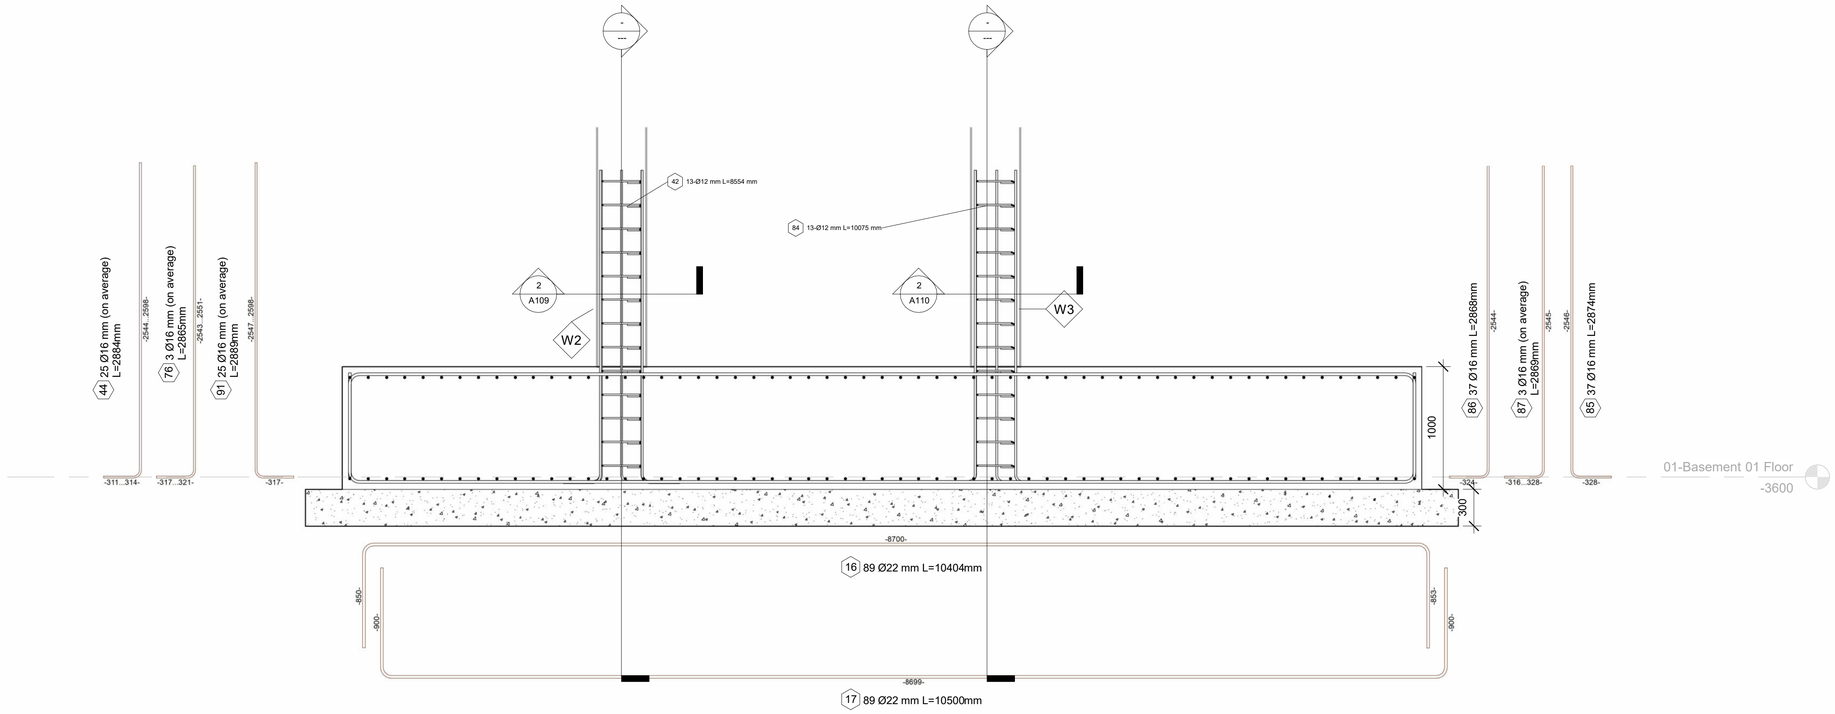

1 RFT F4 SEC 1


1 : 25

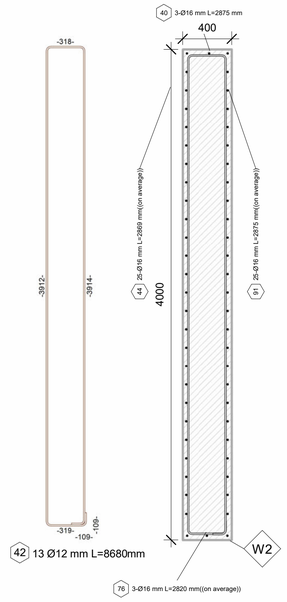

2 RFT W2 SEC

1 : 25

KEY PLAN

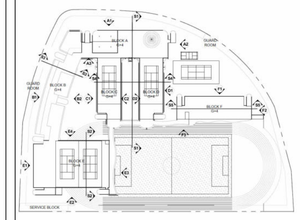


No.	Description	Date

school 1

RFT DETAILING FOR F4 (SHEET1)


Project number	
Date	Issue Date
Drawn by	khalid atef
Checked by	Checker
A109	
Scale	1 : 25

01/11/2026 09:09:26 ص

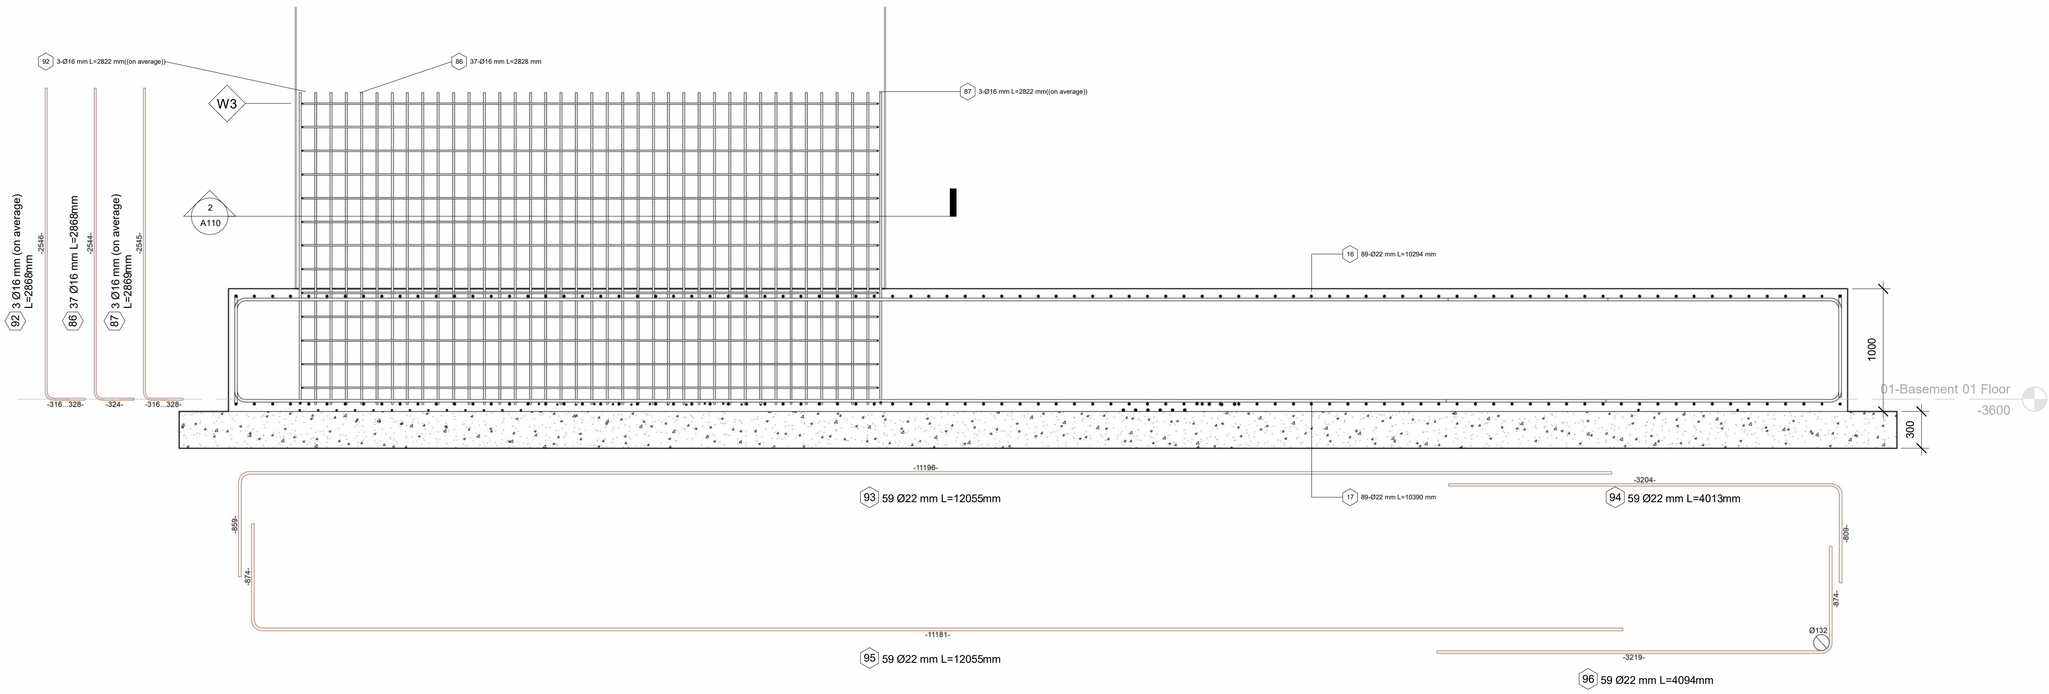

1 RFT F4 SEC 2


1 : 25

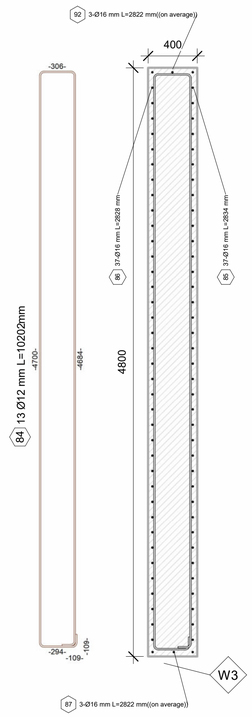

2 RFT W3 SEC

1 : 25

KEY PLAN

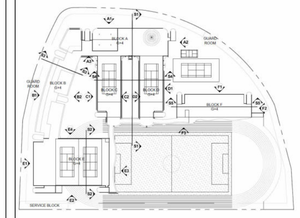


No.	Description	Date

school 1

RFT DETAILING FOR F4 (SHEET2)


Project number	
Date	Issue Date
Drawn by	khalid atef
Checked by	Checker
A110	
Scale	1 : 25

01/11/2026 09:09:39 ص

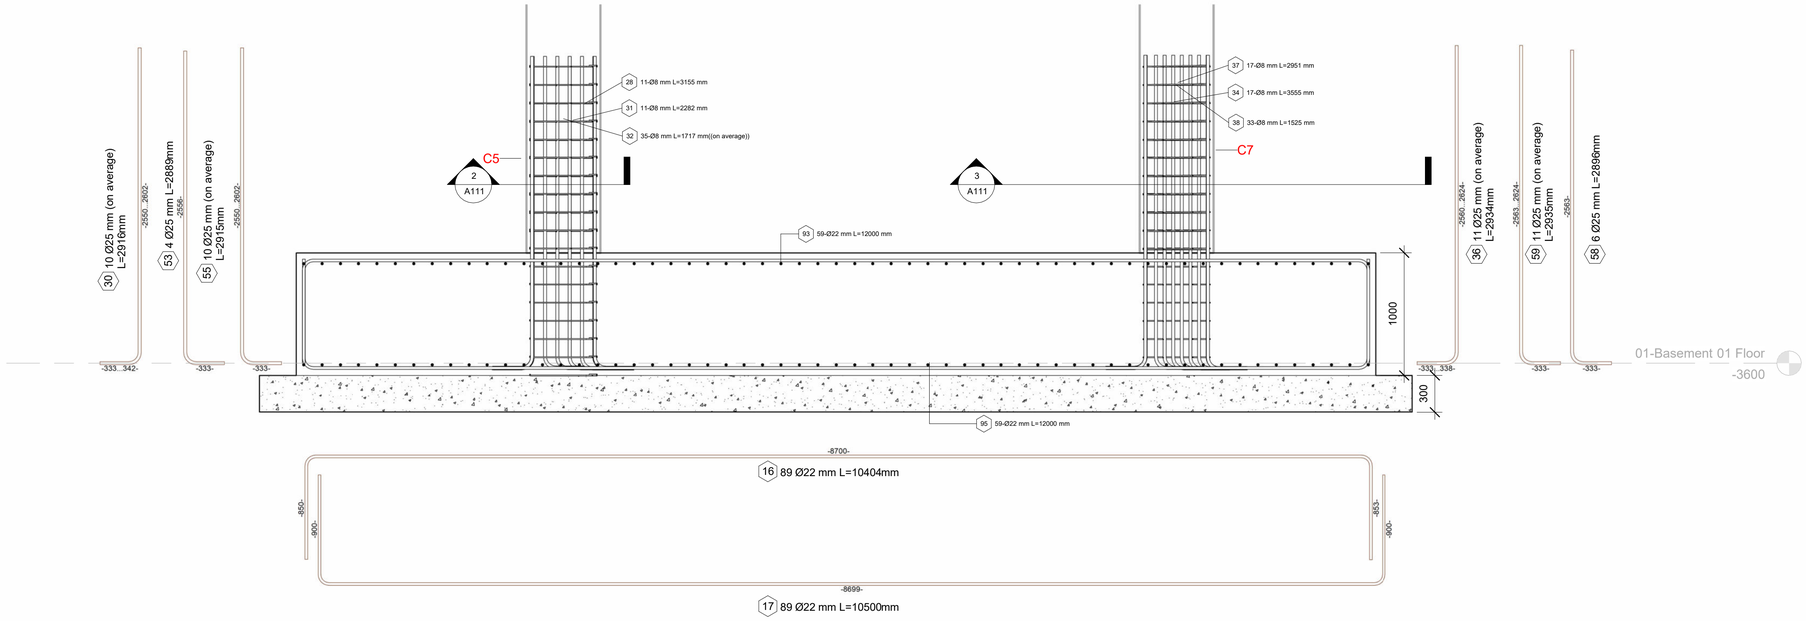


1 RFT F4 SEC 3

1 : 25

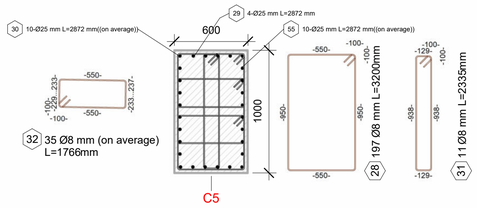

2 RFT C5 SEC


1 : 25

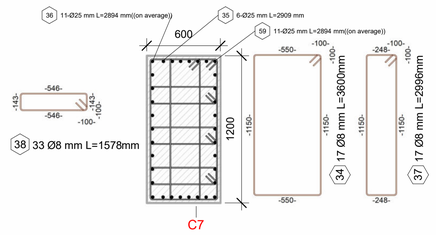

3 RFT C7 SEC

1 : 25

KEY PLAN

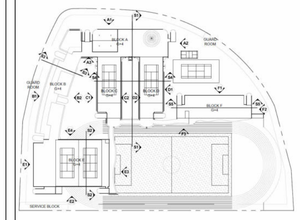


No.	Description	Date

school 1

RFT DETAILING FOR F4 (SHEET3)


Project number	
Date	Issue Date
Drawn by	khalid atef
Checked by	Checker
A111	
Scale	1 : 25

01/11/2026 09:09:52 ص

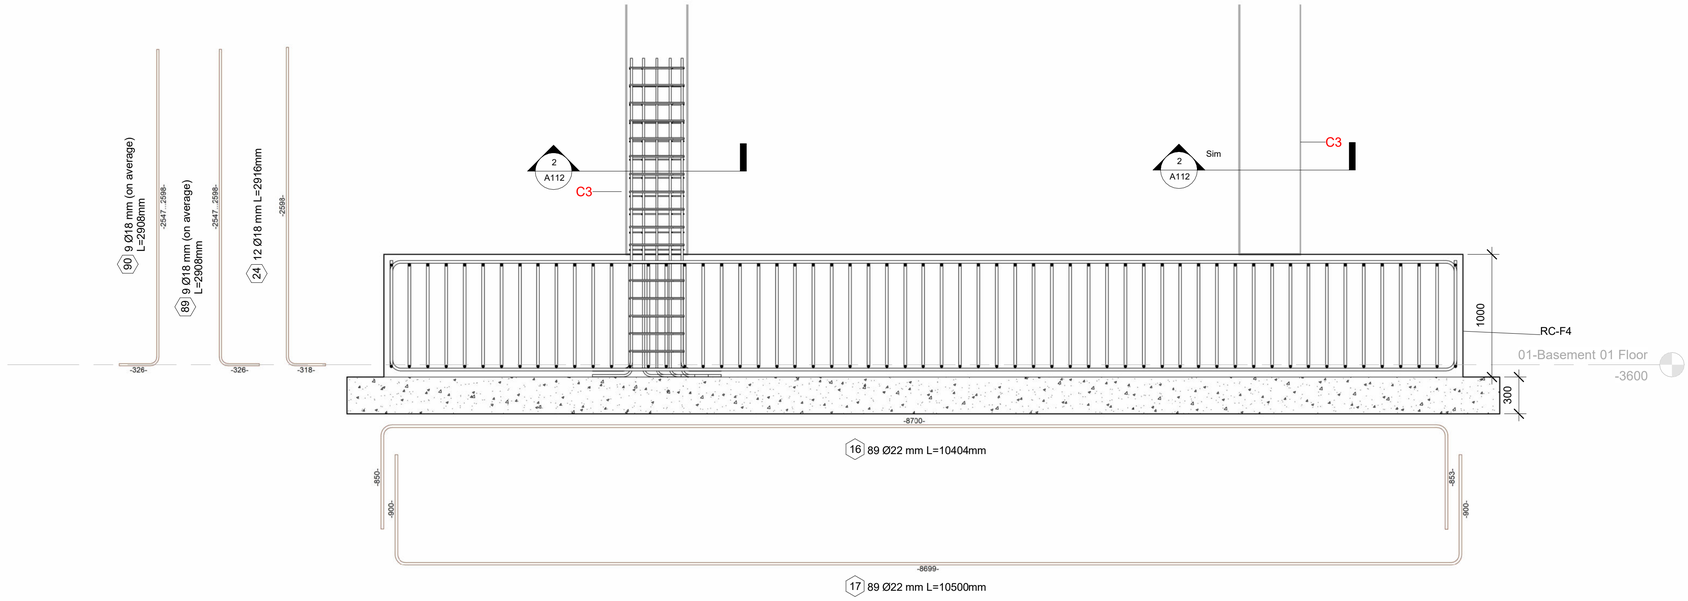

1 RFT F4 SEC 4


1 : 25

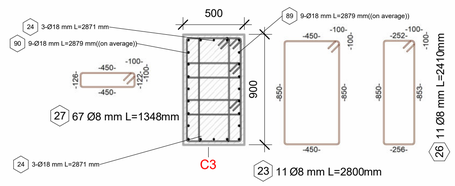

2 RFT C3 SEC

1 : 25

KEY PLAN

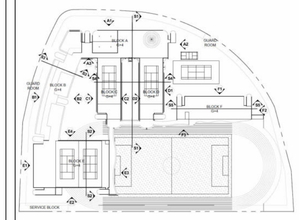


No.	Description	Date

school 1


RFT DETAILING FOR F4 (SHEET4)

Project number	
Date	Issue Date
Drawn by	khalid atef
Checked by	Checker
A112	
Scale	1 : 25


01/11/2026 09:10:04 ص

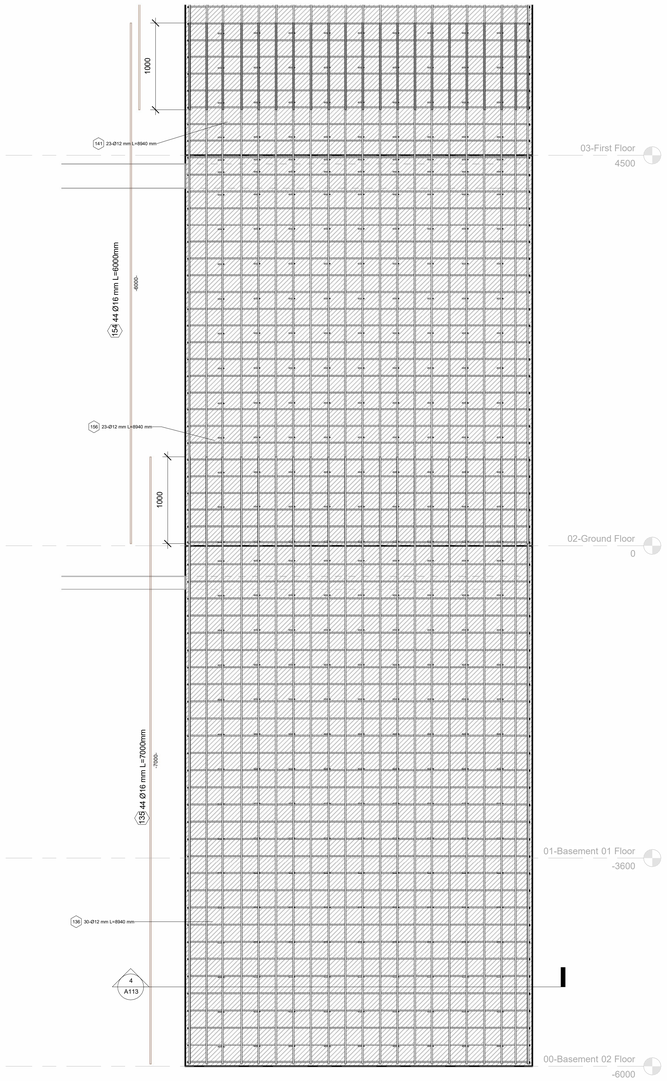


1 W1 RFT-1
1 : 25

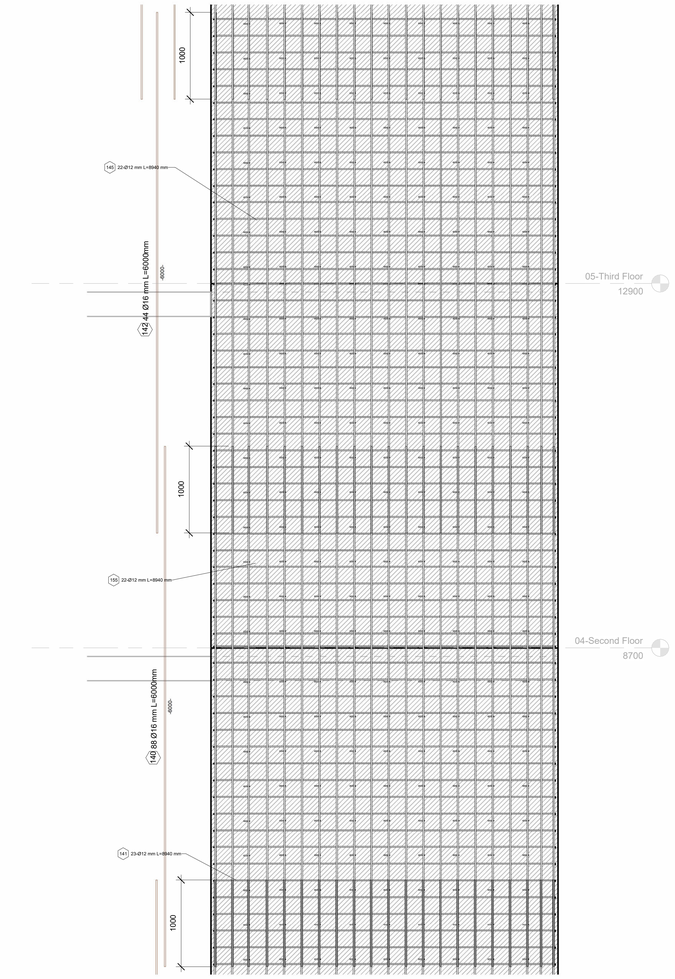

2 W1 RFT-2
1 : 25

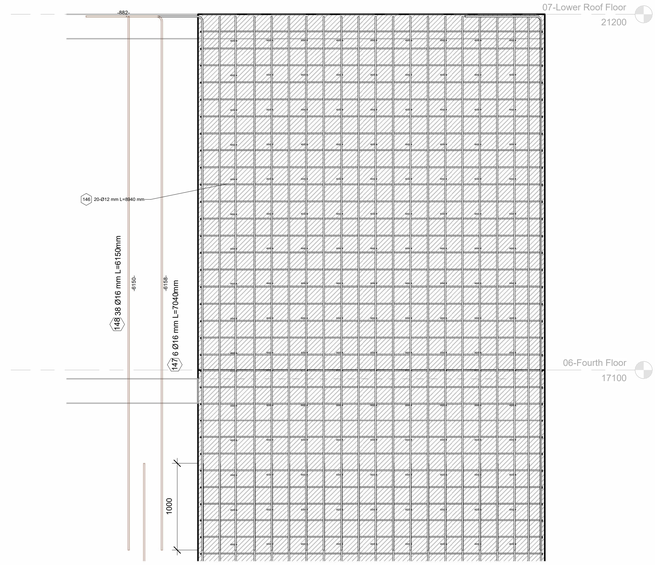


3 W1 RFT-3
1 : 25

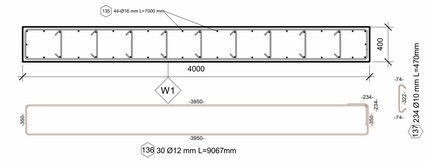

4 W1 CROSS SEC
1 : 25

KEY PLAN

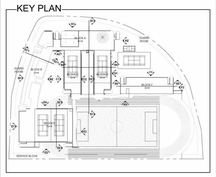

LEGEND

No.	Description	Date


Client Name:

Project Name:
school 1


RFT DETAILING FOR W1

Project number	
Date	**Issue Date**
Drawn by	**khalid atef**
Checked by	**Checker**
Drawing No.	**G07-Z01-S-GN-SEC-00-A113-**
Scale	**1 : 25**


01/11/2026 09:10:30 ص

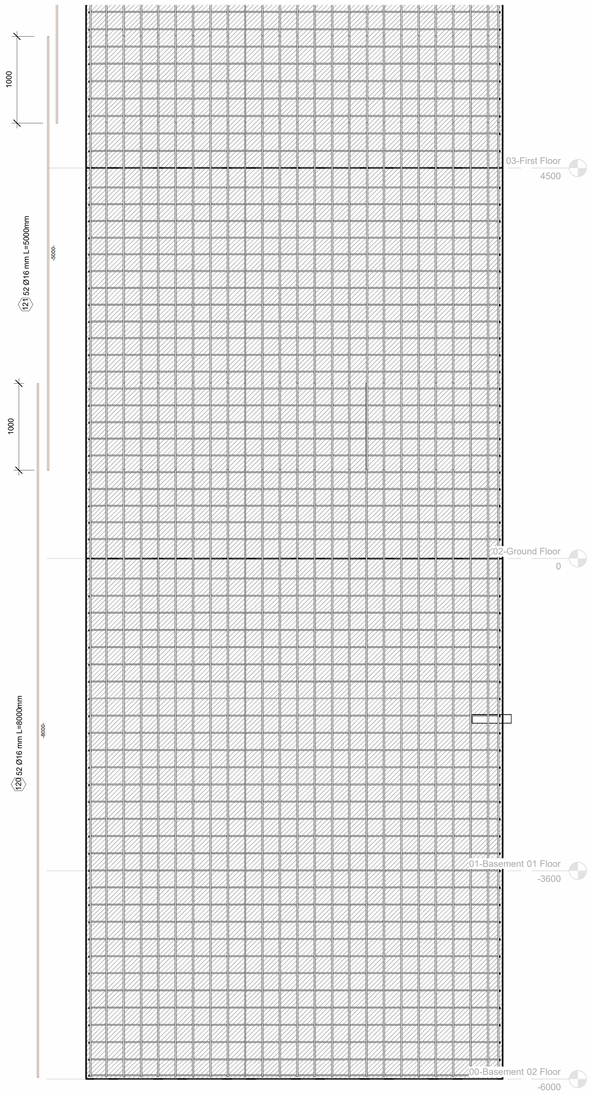


1 W4 RFT-1
1 : 25

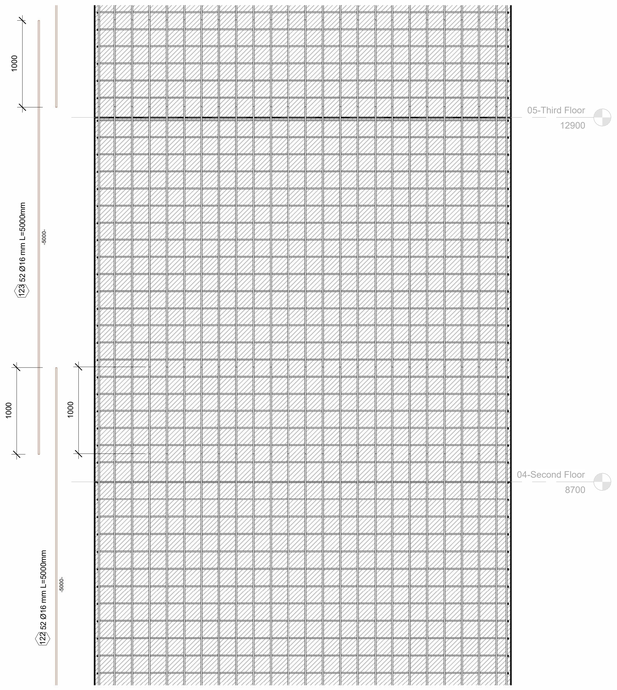

2 W4 RFT-2
1 : 25

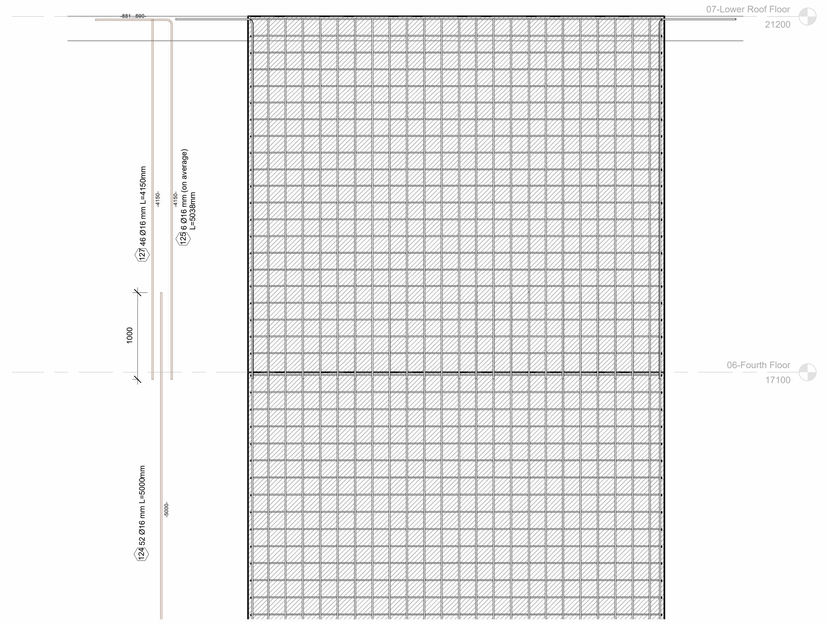


3 W4 RFT-3
1 : 25

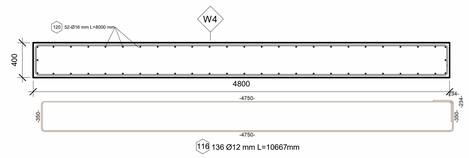

4 W4 CROSS SEC
1 : 25

KEY PLAN

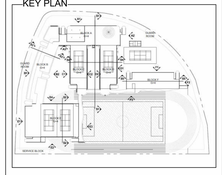

LEGEND

No.	Description	Date


Client Name:

Project Name:
school 1


RFT DETAILING FOR W4

Project number	
Date	**Issue Date**
Drawn by	**khalid atef**
Checked by	**Checker**
Drawing No.	**G07-Z01-S-GN-SEC-00-A114-**
Scale	**1 : 25**


01/11/2026 09:10:55 ص

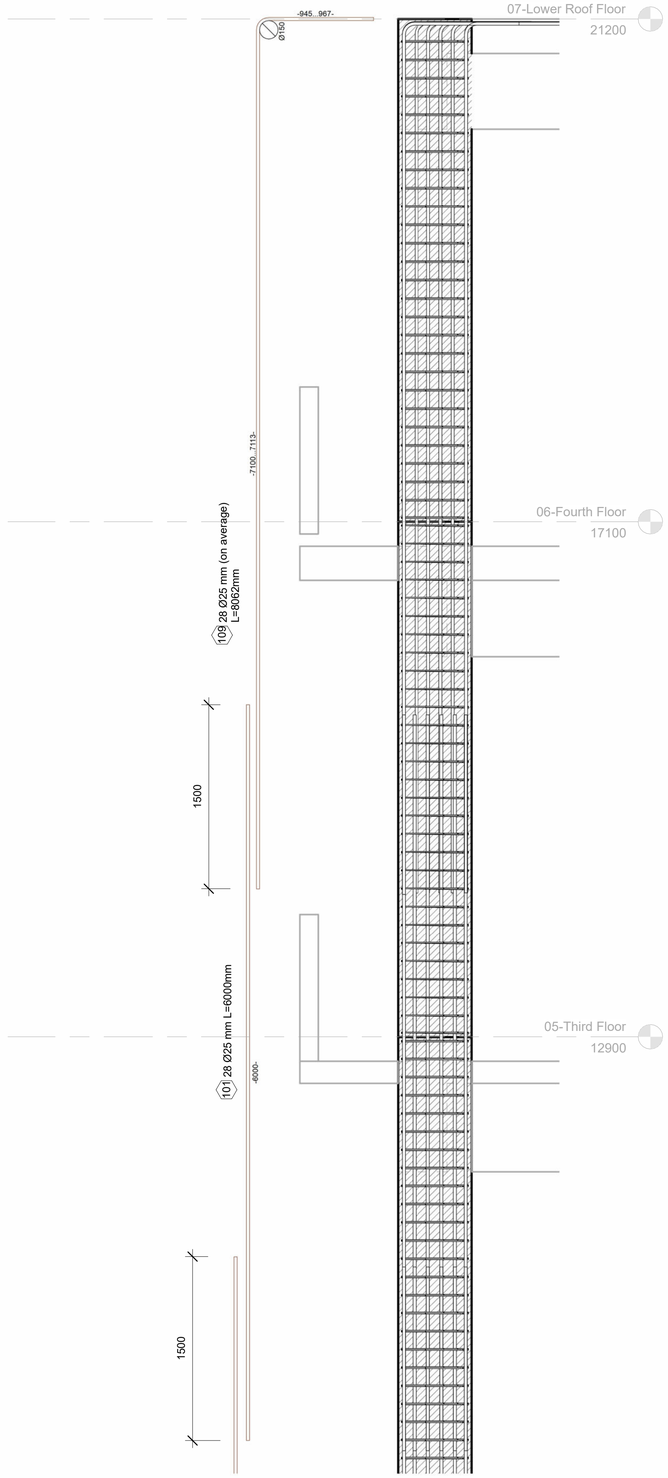


1 C5 RFT-1
1 : 25

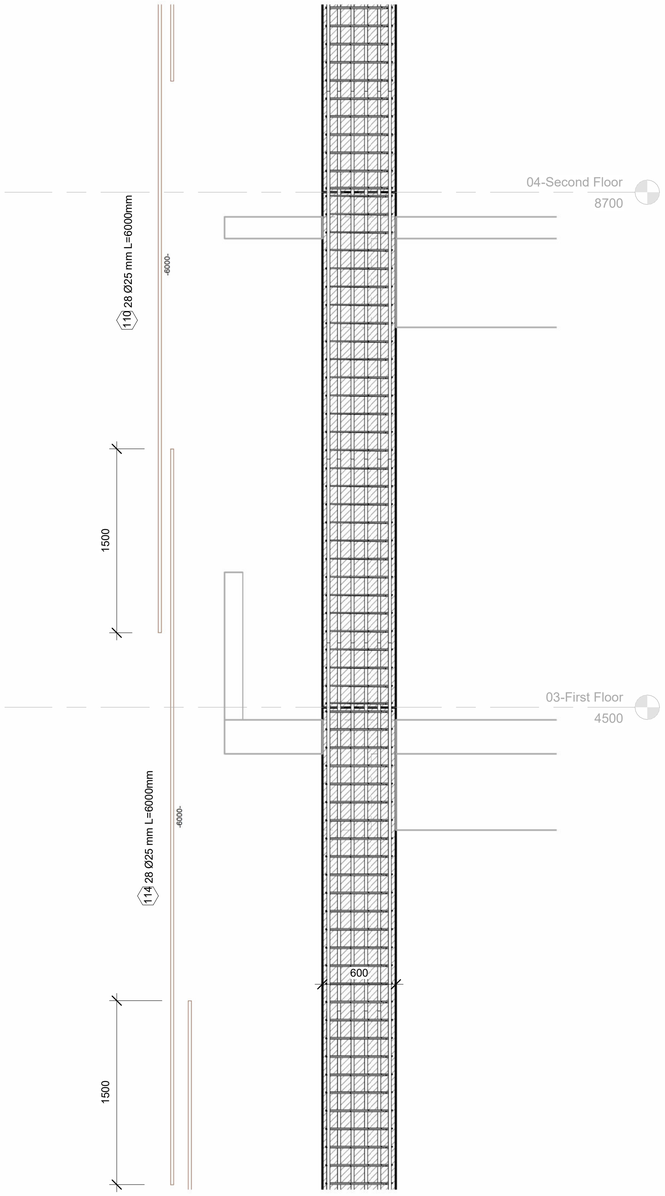

2 C5 RFT-2
1 : 25

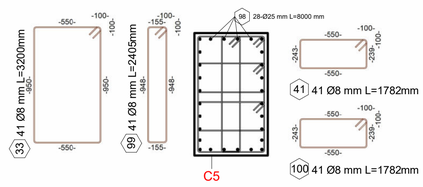


4 C5 CROSS SEC
1 : 25

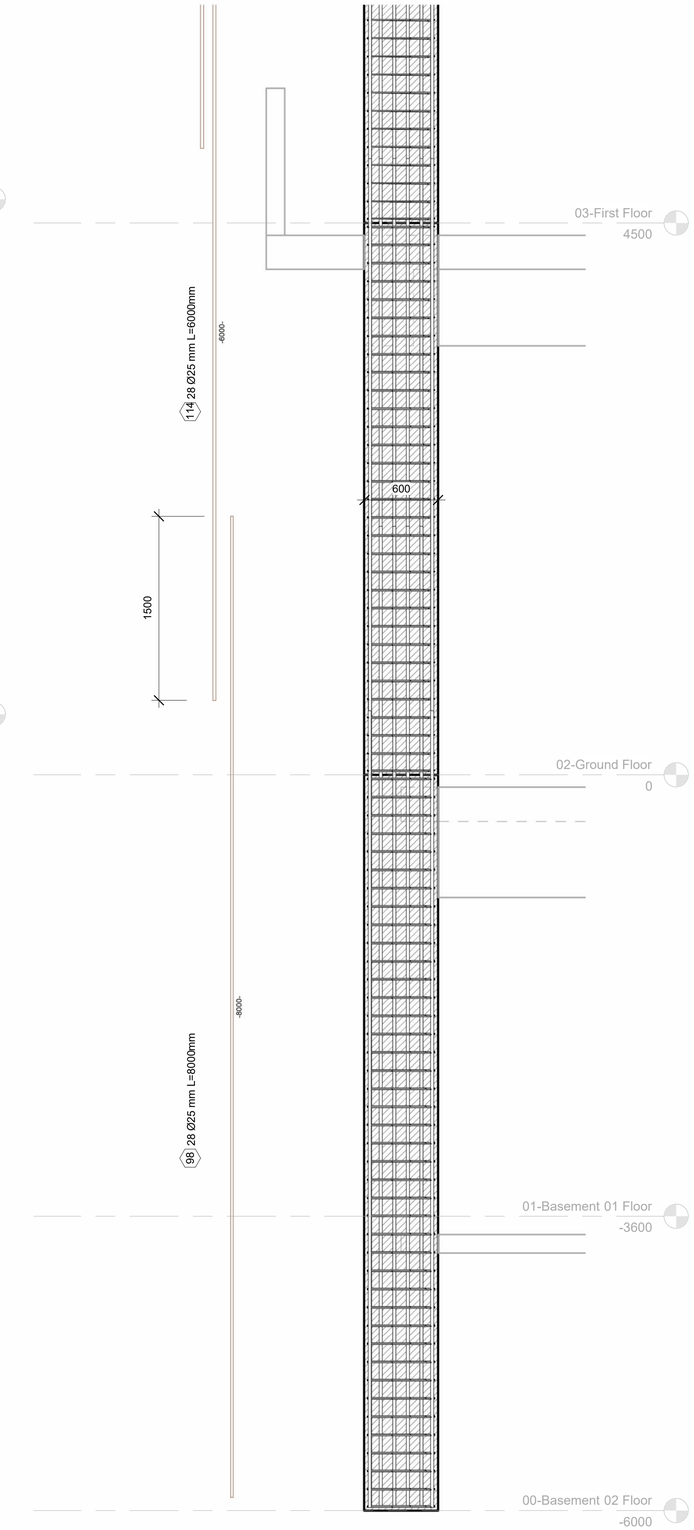

3 C5 RFT-3
1 : 25

KEY PLAN

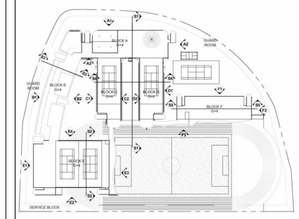

No.	Description	Date

school 1

RFT DETAILING FOR C5


Project number	
Date	Issue Date
Drawn by	khalid atef
Checked by	Checker
	A115
Scale	1 : 25

01/11/2026 09:11:09 ص

KT-R14-G07-Beams BBS							
S_PART ION	Mark	Bar Diameter	Bar Length	Quantity	Total Bar Length	Metric weight	Total Weight
BEAMS	8	8 mm	2139 mm	24	51341 mm	0.395062	0.020283
BEAMS	12	8 mm	2555 mm	45	114964 mm	0.395062	0.045418
BEAMS	14	8 mm	2124 mm	45	95564 mm	0.395062	0.037754
BEAMS	80	8 mm	2555 mm	24	61314 mm	0.395062	0.024223
BEAMS	9	10 mm	4449 mm	4	17798 mm	0.617284	0.010986
BEAMS	13	10 mm	7163 mm	4	28652 mm	0.617284	0.017686
BEAMS	5	12 mm	4059 mm	4	16236 mm	0.888889	0.014432
BEAMS	2	16 mm	4360 mm	4	17440 mm	1.580247	0.02756
BEAMS	3	16 mm	5210 mm	4	20840 mm	1.580247	0.032932
BEAMS	4	16 mm	3602 mm	4	14408 mm	1.580247	0.022768
BEAMS	6	16 mm	8522 mm	4	34088 mm	1.580247	0.053867
BEAMS	10	16 mm	1688 mm	4	6752 mm	1.580247	0.01067
BEAMS	1	18 mm	3252 mm	4	13008 mm	2	0.026016
				174	492404 mm		0.344594

KT-R14-G07-Columns BBS							
S_PART ION	Mark	Bar Diameter	Bar Length	Quantity	Total Bar Length	Metric weight	Total Weight
COULMNS	28	8 mm	3155 mm	145	457439 mm	0.395062	0.180717
COULMNS	33	8 mm	3155 mm	41	129345 mm	0.395062	0.051099
COULMNS	41	8 mm	1737 mm	41	71202 mm	0.395062	0.028129
COULMNS	99	8 mm	2360 mm	41	96760 mm	0.395062	0.038226
COULMNS	100	8 mm	1737 mm	41	71202 mm	0.395062	0.028129
COULMNS	102	8 mm	2362 mm	60	141710 mm	0.395062	0.055984
COULMNS	103	8 mm	1707 mm	62	105860 mm	0.395062	0.041821
COULMNS	104	8 mm	2368 mm	29	68680 mm	0.395062	0.027133
COULMNS	105	8 mm	1724 mm	58	99997 mm	0.395062	0.039505
COULMNS	106	8 mm	2363 mm	29	68532 mm	0.395062	0.027074
COULMNS	107	8 mm	1718 mm	58	99645 mm	0.395062	0.039366
COULMNS	108	8 mm	1726 mm	58	100094 mm	0.395062	0.039544
COULMNS	111	8 mm	2341 mm	27	63196 mm	0.395062	0.024966
COULMNS	112	8 mm	1716 mm	27	46323 mm	0.395062	0.0183
COULMNS	113	8 mm	1695 mm	27	45773 mm	0.395062	0.018083
COULMNS	98	25 mm	8000 mm	28	224000 mm	3.858025	0.864198
COULMNS	101	25 mm	6000 mm	28	168000 mm	3.858025	0.648148
COULMNS	109	25 mm	<varies>	28	223985 mm	3.858025	0.864141
COULMNS	110	25 mm	6000 mm	28	168000 mm	3.858025	0.648148
COULMNS	114	25 mm	6000 mm	28	168000 mm	3.858025	0.648148
				884	2617744 mm		4.330861

KEY PLAN

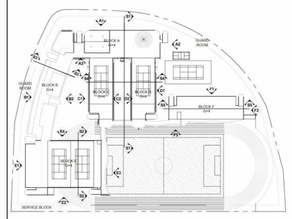

No.	Description	Date
00	Revision 1	Date 1

school 1

BBS Sheet - Coulmns&Beams

Project number

Date — Issue Date

Drawn by — KHALID ATEF

Checked by — Checker

A116

Scale


01/11/2026 09:11:20 ص

KT-R14-G07-Footings BBS							
S_PARTION	Bar Diameter	Mark	Bar Length	Quantity	Total Bar Length	Metric weight	Total Weight
FOUNDATION	8 mm	23	2755 mm	11	30302 mm	0.395062	0.011971
FOUNDATION	8 mm	26	2365 mm	11	26016 mm	0.395062	0.010278
FOUNDATION	8 mm	27	1303 mm	67	87285 mm	0.395062	0.034483
FOUNDATION	8 mm	28	3155 mm	11	34702 mm	0.395062	0.01371
FOUNDATION	8 mm	31	2282 mm	11	25099 mm	0.395062	0.009916
FOUNDATION	8 mm	32	1724 mm	1	1724 mm	0.395062	0.000681
FOUNDATION	8 mm	32	1724 mm	1	1724 mm	0.395062	0.000681
FOUNDATION	8 mm	32	1724 mm	1	1724 mm	0.395062	0.000681
FOUNDATION	8 mm	32	1724 mm	1	1724 mm	0.395062	0.000681
FOUNDATION	8 mm	32	1724 mm	1	1724 mm	0.395062	0.000681
FOUNDATION	8 mm	32	1724 mm	1	1724 mm	0.395062	0.000681
FOUNDATION	8 mm	32	1724 mm	1	1724 mm	0.395062	0.000681
FOUNDATION	8 mm	32	1724 mm	1	1724 mm	0.395062	0.000681
FOUNDATION	8 mm	32	1724 mm	1	1724 mm	0.395062	0.000681
FOUNDATION	8 mm	32	1724 mm	1	1724 mm	0.395062	0.000681
FOUNDATION	8 mm	32	1724 mm	1	1724 mm	0.395062	0.000681
FOUNDATION	8 mm	32	1724 mm	1	1724 mm	0.395062	0.000681
FOUNDATION	8 mm	32	1717 mm	1	1717 mm	0.395062	0.000678
FOUNDATION	8 mm	32	1717 mm	1	1717 mm	0.395062	0.000678
FOUNDATION	8 mm	32	1724 mm	1	1724 mm	0.395062	0.000681
FOUNDATION	8 mm	32	1717 mm	1	1717 mm	0.395062	0.000678
FOUNDATION	8 mm	32	1717 mm	1	1717 mm	0.395062	0.000678
FOUNDATION	8 mm	32	1717 mm	1	1717 mm	0.395062	0.000678
FOUNDATION	8 mm	32	1724 mm	1	1724 mm	0.395062	0.000681
FOUNDATION	8 mm	32	1717 mm	1	1717 mm	0.395062	0.000678
FOUNDATION	8 mm	32	1717 mm	1	1717 mm	0.395062	0.000678
FOUNDATION	8 mm	32	1717 mm	1	1717 mm	0.395062	0.000678
FOUNDATION	8 mm	32	1724 mm	1	1724 mm	0.395062	0.000681
FOUNDATION	8 mm	32	1717 mm	1	1717 mm	0.395062	0.000678
FOUNDATION	8 mm	32	1717 mm	1	1717 mm	0.395062	0.000678

KT-R14-G07-Footings BBS							
S_PARTION	Bar Diameter	Mark	Bar Length	Quantity	Total Bar Length	Metric weight	Total Weight
FOUNDATION	8 mm	32	1717 mm	1	1717 mm	0.395062	0.000678
FOUNDATION	8 mm	32	1724 mm	1	1724 mm	0.395062	0.000681
FOUNDATION	8 mm	32	1717 mm	1	1717 mm	0.395062	0.000678
FOUNDATION	8 mm	32	1717 mm	1	1717 mm	0.395062	0.000678
FOUNDATION	8 mm	32	1717 mm	1	1717 mm	0.395062	0.000678
FOUNDATION	8 mm	32	1717 mm	1	1717 mm	0.395062	0.000678
FOUNDATION	8 mm	32	1717 mm	1	1717 mm	0.395062	0.000678
FOUNDATION	8 mm	32	1717 mm	1	1717 mm	0.395062	0.000678
FOUNDATION	8 mm	32	1717 mm	1	1717 mm	0.395062	0.000678
FOUNDATION	8 mm	34	3555 mm	17	60431 mm	0.395062	0.023874
FOUNDATION	8 mm	37	2951 mm	17	50166 mm	0.395062	0.019819
FOUNDATION	8 mm	38	1525 mm	1	1525 mm	0.395062	0.000602
FOUNDATION	8 mm	38	1525 mm	1	1525 mm	0.395062	0.000602
FOUNDATION	8 mm	38	1525 mm	1	1525 mm	0.395062	0.000602
FOUNDATION	8 mm	38	1525 mm	1	1525 mm	0.395062	0.000602
FOUNDATION	8 mm	38	1525 mm	1	1525 mm	0.395062	0.000602
FOUNDATION	8 mm	38	1525 mm	1	1525 mm	0.395062	0.000602
FOUNDATION	8 mm	38	1525 mm	1	1525 mm	0.395062	0.000602
FOUNDATION	8 mm	38	1528 mm	1	1528 mm	0.395062	0.000604
FOUNDATION	8 mm	38	1525 mm	1	1525 mm	0.395062	0.000602
FOUNDATION	8 mm	38	1525 mm	1	1525 mm	0.395062	0.000602
FOUNDATION	8 mm	38	1525 mm	1	1525 mm	0.395062	0.000602
FOUNDATION	8 mm	38	1525 mm	1	1525 mm	0.395062	0.000602
FOUNDATION	8 mm	38	1525 mm	1	1525 mm	0.395062	0.000602
FOUNDATION	8 mm	38	1525 mm	1	1525 mm	0.395062	0.000602
FOUNDATION	8 mm	38	1528 mm	1	1528 mm	0.395062	0.000604
FOUNDATION	8 mm	38	1525 mm	1	1525 mm	0.395062	0.000602
FOUNDATION	8 mm	38	1528 mm	1	1528 mm	0.395062	0.000604
FOUNDATION	8 mm	38	1525 mm	1	1525 mm	0.395062	0.000602

KT-R14-G07-Footings BBS							
S_PARTION	Bar Diameter	Mark	Bar Length	Quantity	Total Bar Length	Metric weight	Total Weight
FOUNDATION	8 mm	38	1528 mm	1	1528 mm	0.395062	0.000604
FOUNDATION	8 mm	38	1525 mm	1	1525 mm	0.395062	0.000602
FOUNDATION	8 mm	38	1528 mm	1	1528 mm	0.395062	0.000604
FOUNDATION	8 mm	38	1525 mm	1	1525 mm	0.395062	0.000602
FOUNDATION	8 mm	38	1528 mm	1	1528 mm	0.395062	0.000604
FOUNDATION	8 mm	38	1525 mm	1	1525 mm	0.395062	0.000602
FOUNDATION	8 mm	38	1528 mm	1	1528 mm	0.395062	0.000604
FOUNDATION	8 mm	38	1525 mm	1	1525 mm	0.395062	0.000602
FOUNDATION	8 mm	38	1528 mm	1	1528 mm	0.395062	0.000604
FOUNDATION	8 mm	38	1525 mm	1	1525 mm	0.395062	0.000602
FOUNDATION	8 mm	38	1528 mm	1	1528 mm	0.395062	0.000604
FOUNDATION	12 mm	42	8554 mm	13	111201 mm	0.888889	0.098846
FOUNDATION	12 mm	84	10075 mm	13	130979 mm	0.888889	0.116426
FOUNDATION	16 mm	40	2875 mm	3	8624 mm	1.580247	0.013629
FOUNDATION	16 mm	44	2872 mm	1	2872 mm	1.580247	0.004538
FOUNDATION	16 mm	44	2869 mm	1	2869 mm	1.580247	0.004533
FOUNDATION	16 mm	44	2869 mm	1	2869 mm	1.580247	0.004533
FOUNDATION	16 mm	44	2869 mm	1	2869 mm	1.580247	0.004533
FOUNDATION	16 mm	44	2869 mm	1	2869 mm	1.580247	0.004533
FOUNDATION	16 mm	44	2869 mm	1	2869 mm	1.580247	0.004533
FOUNDATION	16 mm	44	2869 mm	1	2869 mm	1.580247	0.004533
FOUNDATION	16 mm	44	2869 mm	1	2869 mm	1.580247	0.004533
FOUNDATION	16 mm	44	2869 mm	1	2869 mm	1.580247	0.004533
FOUNDATION	16 mm	44	2822 mm	1	2822 mm	1.580247	0.00446

KEY PLAN

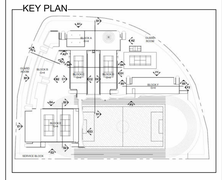

LEGEND

No.	Description	Date
00	Revision 1	Date 1

Client Name:

Project Name:

school 1

BBS Sheet-Foundation-1

Project number

Date **Issue Date**

Drawn by **KHALID ATEF**

Checked by **Checker**

Drawing No.

G07-Z01-S-GN-SC-ZZ-A117-00

Scale


01/11/2026 09:11:44 ص

KT-R14-G07-Footings BBS							
S_PARTION	Bar Diameter	Mark	Bar Length	Quantity	Total Bar Length	Metric weight	Total Weight
FOUNDATION	16 mm	44	2815 mm	1	2815 mm	1.580247	0.004448
FOUNDATION	16 mm	44	2823 mm	1	2823 mm	1.580247	0.004461
FOUNDATION	16 mm	44	2822 mm	1	2822 mm	1.580247	0.00446
FOUNDATION	16 mm	44	2822 mm	1	2822 mm	1.580247	0.00446
FOUNDATION	16 mm	44	2820 mm	1	2820 mm	1.580247	0.004457
FOUNDATION	16 mm	44	2823 mm	1	2823 mm	1.580247	0.004461
FOUNDATION	16 mm	44	2819 mm	1	2819 mm	1.580247	0.004454
FOUNDATION	16 mm	44	2820 mm	1	2820 mm	1.580247	0.004457
FOUNDATION	16 mm	44	2819 mm	1	2819 mm	1.580247	0.004455
FOUNDATION	16 mm	44	2819 mm	1	2819 mm	1.580247	0.004455
FOUNDATION	16 mm	44	2820 mm	1	2820 mm	1.580247	0.004457
FOUNDATION	16 mm	44	2818 mm	1	2818 mm	1.580247	0.004452
FOUNDATION	16 mm	76	2828 mm	1	2828 mm	1.580247	0.004469
FOUNDATION	16 mm	76	2820 mm	1	2820 mm	1.580247	0.004456
FOUNDATION	16 mm	76	2827 mm	1	2827 mm	1.580247	0.004468
FOUNDATION	16 mm	85	2834 mm	37	104871 mm	1.580247	0.165722
FOUNDATION	16 mm	86	2828 mm	37	104651 mm	1.580247	0.165375
FOUNDATION	16 mm	87	2832 mm	1	2832 mm	1.580247	0.004475
FOUNDATION	16 mm	87	2822 mm	1	2822 mm	1.580247	0.00446
FOUNDATION	16 mm	87	2834 mm	1	2834 mm	1.580247	0.004478
FOUNDATION	16 mm	91	2875 mm	1	2875 mm	1.580247	0.004543
FOUNDATION	16 mm	91	2875 mm	1	2875 mm	1.580247	0.004543
FOUNDATION	16 mm	91	2875 mm	1	2875 mm	1.580247	0.004543
FOUNDATION	16 mm	91	2875 mm	1	2875 mm	1.580247	0.004543
FOUNDATION	16 mm	91	2875 mm	1	2875 mm	1.580247	0.004543
FOUNDATION	16 mm	91	2875 mm	1	2875 mm	1.580247	0.004543
FOUNDATION	16 mm	91	2875 mm	1	2875 mm	1.580247	0.004543
FOUNDATION	16 mm	91	2875 mm	1	2875 mm	1.580247	0.004543
FOUNDATION	16 mm	91	2875 mm	1	2875 mm	1.580247	0.004543

KT-R14-G07-Footings BBS							
S_PARTION	Bar Diameter	Mark	Bar Length	Quantity	Total Bar Length	Metric weight	Total Weight
FOUNDATION	16 mm	91	2875 mm	1	2875 mm	1.580247	0.004543
FOUNDATION	16 mm	91	2875 mm	1	2875 mm	1.580247	0.004543
FOUNDATION	16 mm	91	2824 mm	1	2824 mm	1.580247	0.004462
FOUNDATION	16 mm	91	2827 mm	1	2827 mm	1.580247	0.004468
FOUNDATION	16 mm	91	2828 mm	1	2828 mm	1.580247	0.004469
FOUNDATION	16 mm	91	2825 mm	1	2825 mm	1.580247	0.004463
FOUNDATION	16 mm	91	2825 mm	1	2825 mm	1.580247	0.004465
FOUNDATION	16 mm	91	2828 mm	1	2828 mm	1.580247	0.004469
FOUNDATION	16 mm	91	2825 mm	1	2825 mm	1.580247	0.004463
FOUNDATION	16 mm	91	2825 mm	1	2825 mm	1.580247	0.004463
FOUNDATION	16 mm	91	2829 mm	1	2829 mm	1.580247	0.004471
FOUNDATION	16 mm	91	2822 mm	1	2822 mm	1.580247	0.004459
FOUNDATION	16 mm	91	2822 mm	1	2822 mm	1.580247	0.004459
FOUNDATION	16 mm	91	2827 mm	1	2827 mm	1.580247	0.004468
FOUNDATION	16 mm	91	2828 mm	1	2828 mm	1.580247	0.004469
FOUNDATION	16 mm	92	2828 mm	1	2828 mm	1.580247	0.00447
FOUNDATION	16 mm	92	2822 mm	1	2822 mm	1.580247	0.00446
FOUNDATION	16 mm	92	2834 mm	1	2834 mm	1.580247	0.004479
FOUNDATION	18 mm	22	2879 mm	1	2879 mm	2	0.005758
FOUNDATION	18 mm	22	2871 mm	1	2871 mm	2	0.005742
FOUNDATION	18 mm	22	2871 mm	1	2871 mm	2	0.005742
FOUNDATION	18 mm	22	2871 mm	1	2871 mm	2	0.005742
FOUNDATION	18 mm	22	2879 mm	1	2879 mm	2	0.005758
FOUNDATION	18 mm	22	2879 mm	1	2879 mm	2	0.005758
FOUNDATION	18 mm	22	2871 mm	1	2871 mm	2	0.005742
FOUNDATION	18 mm	22	2871 mm	1	2871 mm	2	0.005742
FOUNDATION	18 mm	22	2871 mm	1	2871 mm	2	0.005742
FOUNDATION	18 mm	22	2879 mm	1	2879 mm	2	0.005758
FOUNDATION	18 mm	24	2871 mm	1	2871 mm	2	0.005742
FOUNDATION	18 mm	24	2871 mm	1	2871 mm	2	0.005742

KT-R14-G07-Footings BBS							
S_PARTION	Bar Diameter	Mark	Bar Length	Quantity	Total Bar Length	Metric weight	Total Weight
FOUNDATION	18 mm	24	2871 mm	1	2871 mm	2	0.005742
FOUNDATION	18 mm	24	2871 mm	1	2871 mm	2	0.005742
FOUNDATION	18 mm	24	2871 mm	1	2871 mm	2	0.005742
FOUNDATION	18 mm	24	2871 mm	3	8613 mm	2	0.017226
FOUNDATION	18 mm	24	2871 mm	3	8613 mm	2	0.017226
FOUNDATION	18 mm	25	2879 mm	1	2879 mm	2	0.005758
FOUNDATION	18 mm	25	2879 mm	1	2879 mm	2	0.005758
FOUNDATION	18 mm	25	2879 mm	1	2879 mm	2	0.005758
FOUNDATION	18 mm	25	2879 mm	1	2879 mm	2	0.005758
FOUNDATION	18 mm	89	2879 mm	1	2879 mm	2	0.005758
FOUNDATION	18 mm	89	2879 mm	1	2879 mm	2	0.005758
FOUNDATION	18 mm	89	2879 mm	1	2879 mm	2	0.005758
FOUNDATION	18 mm	89	2879 mm	1	2879 mm	2	0.005758
FOUNDATION	18 mm	89	2879 mm	1	2879 mm	2	0.005758
FOUNDATION	18 mm	89	2828 mm	1	2828 mm	2	0.005656
FOUNDATION	18 mm	89	2834 mm	1	2834 mm	2	0.005667
FOUNDATION	18 mm	89	2834 mm	1	2834 mm	2	0.005667
FOUNDATION	18 mm	89	2879 mm	1	2879 mm	2	0.005758
FOUNDATION	18 mm	90	2879 mm	1	2879 mm	2	0.005758
FOUNDATION	18 mm	90	2879 mm	1	2879 mm	2	0.005758
FOUNDATION	18 mm	90	2879 mm	1	2879 mm	2	0.005758
FOUNDATION	18 mm	90	2879 mm	1	2879 mm	2	0.005758
FOUNDATION	18 mm	90	2879 mm	1	2879 mm	2	0.005758
FOUNDATION	18 mm	90	2833 mm	1	2833 mm	2	0.005665
FOUNDATION	18 mm	90	2828 mm	1	2828 mm	2	0.005656
FOUNDATION	18 mm	90	2829 mm	1	2829 mm	2	0.005658
FOUNDATION	18 mm	90	2879 mm	1	2879 mm	2	0.005758
FOUNDATION	22 mm	16	10294 mm	89	916132 mm	2.987654	2.737085
FOUNDATION	22 mm	17	10390 mm	89	924689 mm	2.987654	2.76265

KEY PLAN

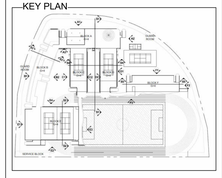

LEGEND

No.	Description	Date
00	Revision 1	Date 1

Client Name:

Project Name:

school 1

BBS Sheet-Foundation-2

Project number

Date **Issue Date**

Drawn by **Author**

Checked by **Checker**

Drawing No.

G07-Z01-S-GN-SC-ZZ-A118-00


Scale

01/11/2028 09:12:07 ص

KT-R14-G07-Footings BBS							
S_PARTION	Bar Diameter	Mark	Bar Length	Quantity	Total Bar Length	Metric weight	Total Weight
FOUNDATION	25 mm	29	2872 mm	4	11488 mm	3.858025	0.04432
FOUNDATION	25 mm	30	2833 mm	1	2833 mm	3.858025	0.010929
FOUNDATION	25 mm	30	2825 mm	1	2825 mm	3.858025	0.010901
FOUNDATION	25 mm	30	2821 mm	1	2821 mm	3.858025	0.010883
FOUNDATION	25 mm	30	2822 mm	1	2822 mm	3.858025	0.010889
FOUNDATION	25 mm	30	2872 mm	1	2872 mm	3.858025	0.01108
FOUNDATION	25 mm	30	2872 mm	1	2872 mm	3.858025	0.01108
FOUNDATION	25 mm	30	2872 mm	1	2872 mm	3.858025	0.01108
FOUNDATION	25 mm	30	2872 mm	1	2872 mm	3.858025	0.01108
FOUNDATION	25 mm	30	2872 mm	1	2872 mm	3.858025	0.01108
FOUNDATION	25 mm	30	2872 mm	1	2872 mm	3.858025	0.01108
FOUNDATION	25 mm	35	2894 mm	1	2894 mm	3.858025	0.011165
FOUNDATION	25 mm	35	2909 mm	1	2909 mm	3.858025	0.011225
FOUNDATION	25 mm	35	2909 mm	1	2909 mm	3.858025	0.011225
FOUNDATION	25 mm	35	2909 mm	1	2909 mm	3.858025	0.011225
FOUNDATION	25 mm	35	2907 mm	1	2907 mm	3.858025	0.011213
FOUNDATION	25 mm	35	2909 mm	1	2909 mm	3.858025	0.011225
FOUNDATION	25 mm	36	2835 mm	1	2835 mm	3.858025	0.010938
FOUNDATION	25 mm	36	2831 mm	1	2831 mm	3.858025	0.010924
FOUNDATION	25 mm	36	2830 mm	1	2830 mm	3.858025	0.010918
FOUNDATION	25 mm	36	2833 mm	1	2833 mm	3.858025	0.010929
FOUNDATION	25 mm	36	2894 mm	1	2894 mm	3.858025	0.011165
FOUNDATION	25 mm	36	2894 mm	1	2894 mm	3.858025	0.011165
FOUNDATION	25 mm	53	2826 mm	1	2826 mm	3.858025	0.010903
FOUNDATION	25 mm	53	2825 mm	1	2825 mm	3.858025	0.010898

KT-R14-G07-Footings BBS							
S_PARTION	Bar Diameter	Mark	Bar Length	Quantity	Total Bar Length	Metric weight	Total Weight
FOUNDATION	25 mm	53	2823 mm	1	2823 mm	3.858025	0.010892
FOUNDATION	25 mm	53	2819 mm	1	2819 mm	3.858025	0.010874
FOUNDATION	25 mm	55	2824 mm	1	2824 mm	3.858025	0.010895
FOUNDATION	25 mm	55	2826 mm	1	2826 mm	3.858025	0.010903
FOUNDATION	25 mm	55	2823 mm	1	2823 mm	3.858025	0.010892
FOUNDATION	25 mm	55	2820 mm	1	2820 mm	3.858025	0.01088
FOUNDATION	25 mm	55	2872 mm	1	2872 mm	3.858025	0.01108
FOUNDATION	25 mm	55	2872 mm	1	2872 mm	3.858025	0.01108
FOUNDATION	25 mm	55	2872 mm	1	2872 mm	3.858025	0.01108
FOUNDATION	25 mm	55	2872 mm	1	2872 mm	3.858025	0.01108
FOUNDATION	25 mm	55	2872 mm	1	2872 mm	3.858025	0.01108
FOUNDATION	25 mm	55	2872 mm	1	2872 mm	3.858025	0.01108
FOUNDATION	25 mm	58	2834 mm	1	2834 mm	3.858025	0.010933
FOUNDATION	25 mm	58	2836 mm	1	2836 mm	3.858025	0.010942
FOUNDATION	25 mm	58	2835 mm	1	2835 mm	3.858025	0.010936
FOUNDATION	25 mm	58	2835 mm	1	2835 mm	3.858025	0.010939
FOUNDATION	25 mm	58	2832 mm	1	2832 mm	3.858025	0.010924
FOUNDATION	25 mm	58	2832 mm	1	2832 mm	3.858025	0.010926
FOUNDATION	25 mm	59	2833 mm	1	2833 mm	3.858025	0.01093
FOUNDATION	25 mm	59	2835 mm	1	2835 mm	3.858025	0.010939
FOUNDATION	25 mm	59	2835 mm	1	2835 mm	3.858025	0.010936
FOUNDATION	25 mm	59	2835 mm	1	2835 mm	3.858025	0.010936
FOUNDATION	25 mm	59	2894 mm	1	2894 mm	3.858025	0.011165
FOUNDATION	25 mm	59	2894 mm	1	2894 mm	3.858025	0.011165
FOUNDATION	25 mm	59	2894 mm	1	2894 mm	3.858025	0.011165
FOUNDATION	25 mm	59	2894 mm	1	2894 mm	3.858025	0.011165
FOUNDATION	25 mm	59	2894 mm	1	2894 mm	3.858025	0.011165
FOUNDATION	25 mm	59	2894 mm	1	2894 mm	3.858025	0.011165
				659	3197187 mm		7.429718

KEY PLAN

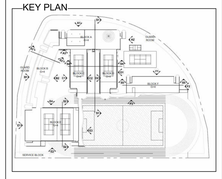

LEGEND

No.	Description	Date
00	Revision 1	Date 1

Client Name:

Project Name:

school 1

BBS Sheet-Foundation-3

Project number

Date **Issue Date**

Drawn by **Author**

Checked by **Checker**

Drawing No.

G07-Z01-S-GN-SC-ZZ-A119-00

Scale

01/11/2026 09:12:31 ص