
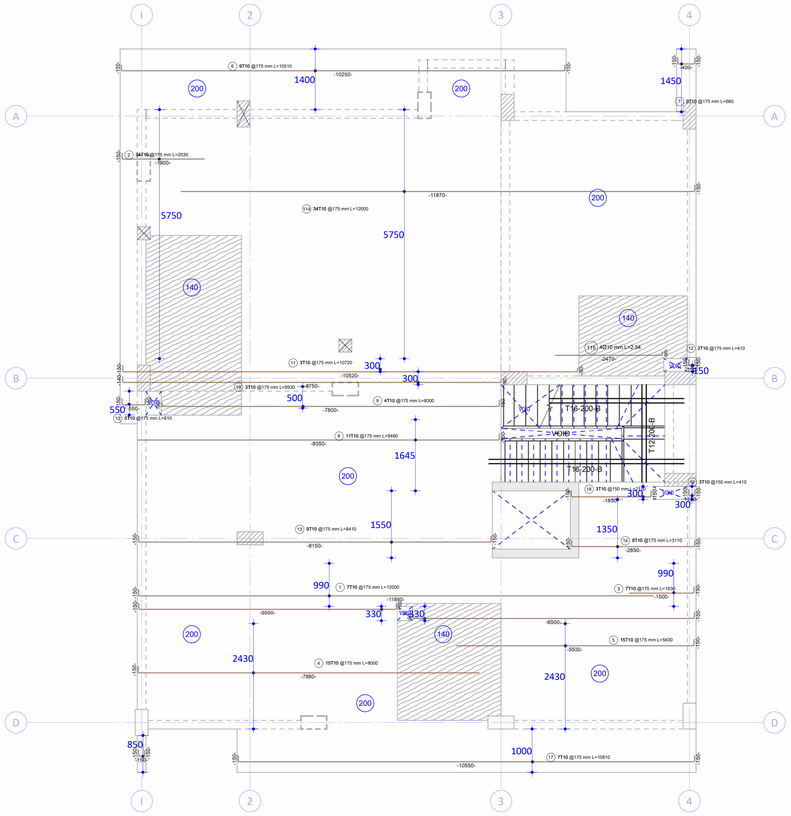


1 **FIRST FLOOR-MESH-BOT-X**
1 : 50

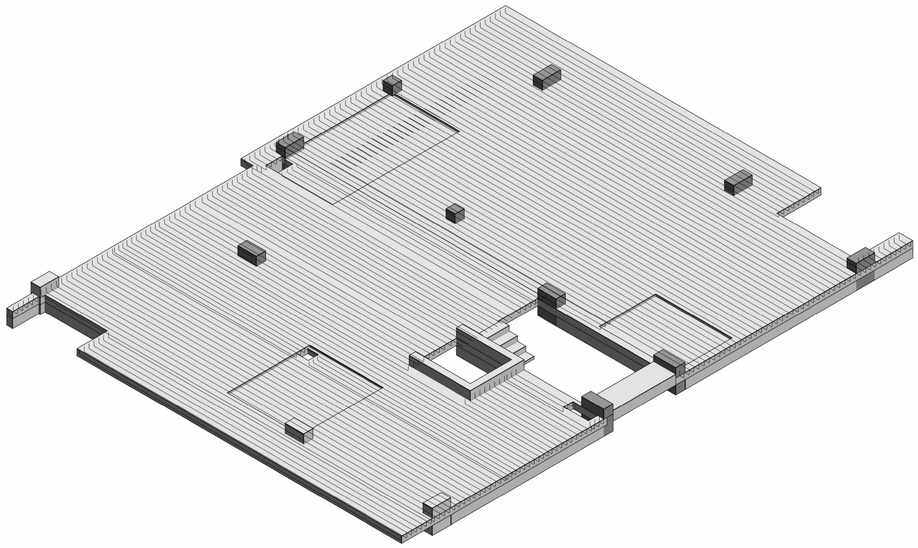

2 **RFT-MESH-BOT X**


04-MESH-BOT-X Schedule							
S_PARTION	Bar Diameter	Mark	Bar Length	Quantity	Total Bar Length	METRIC WEIGHT	WEIGHT
MESH-BOT-X	10 mm	1	12000 mm	7	84000 mm	0.617284	0.051852
MESH-BOT-X	10 mm	2	2030 mm	34	69020 mm	0.617284	0.042605
MESH-BOT-X	10 mm	3	1630 mm	7	11410 mm	0.617284	0.007043
MESH-BOT-X	10 mm	4	8000 mm	15	120000 mm	0.617284	0.074074
MESH-BOT-X	10 mm	5	5630 mm	15	84450 mm	0.617284	0.05213
MESH-BOT-X	10 mm	6	10510 mm	9	94590 mm	0.617284	0.058389
MESH-BOT-X	10 mm	7	660 mm	9	5940 mm	0.617284	0.003667
MESH-BOT-X	10 mm	8	8480 mm	11	93280 mm	0.617284	0.05758
MESH-BOT-X	10 mm	9	8000 mm	4	32000 mm	0.617284	0.019753
MESH-BOT-X	10 mm	10	810 mm	5	4050 mm	0.617284	0.0025
MESH-BOT-X	10 mm	11	10720 mm	3	32160 mm	0.617284	0.019852
MESH-BOT-X	10 mm	12	410 mm	2	820 mm	0.617284	0.000506
MESH-BOT-X	10 mm	12	410 mm	3	1230 mm	0.617284	0.000759
MESH-BOT-X	10 mm	12	410 mm	6	2460 mm	0.617284	0.001519
MESH-BOT-X	10 mm	13	8410 mm	9	75690 mm	0.617284	0.046722
MESH-BOT-X	10 mm	14	3110 mm	9	27990 mm	0.617284	0.017278
MESH-BOT-X	10 mm	15	6700 mm	3	20100 mm	0.617284	0.012407
MESH-BOT-X	10 mm	16	6210 mm	3	18630 mm	0.617284	0.0115
MESH-BOT-X	10 mm	17	10810 mm	7	75670 mm	0.617284	0.04671
MESH-BOT-X	10 mm	18	2110 mm	3	6330 mm	0.617284	0.003907
MESH-BOT-X	10 mm	19	8930 mm	3	26790 mm	0.617284	0.016537
MESH-BOT-X	10 mm	114	12000 mm	34	408000 mm	0.617284	0.251852
MESH-BOT-X	10 mm	115	2540 mm	4	10160 mm	0.617284	0.006272
					1304770 mm		0.805414

CONSULTANT

CONTRACTOR

NOTES

KEY PLAN

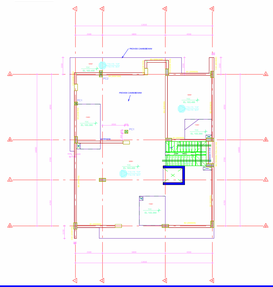

REVISION SCHEDULE

REV	Date	ISSUED FOR	Issued by	Issued to

DISCIPLINE

SHEET TILLE

RFT-MESH-BOT-X


DRW BY : KHALED ATEF

CHK BY : Checker

SCALE


1 : 50

REVISION

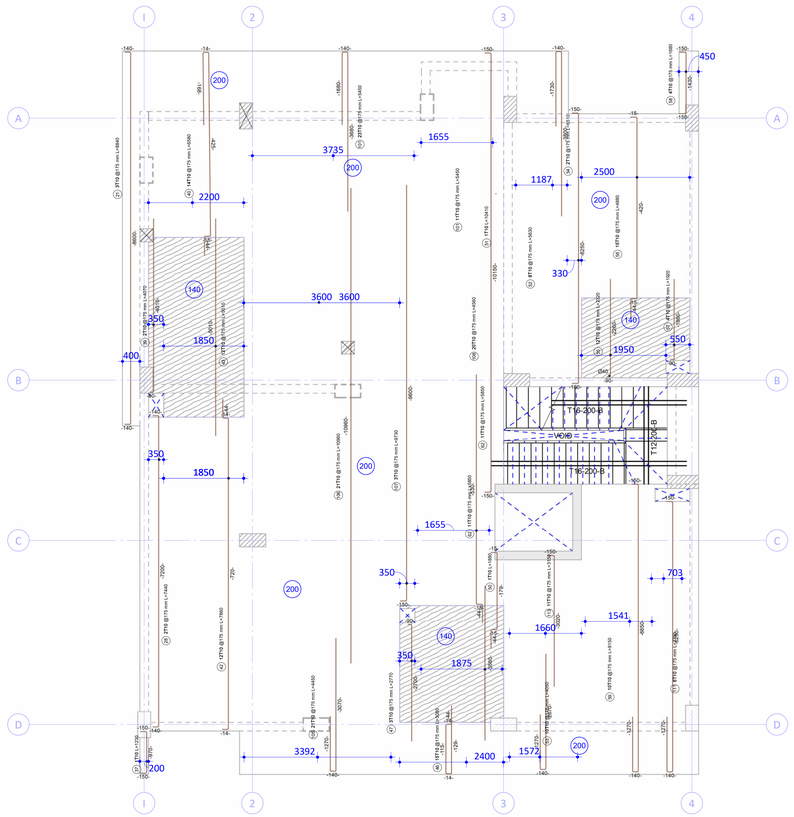

1 **FIRST FLOOR-MESH-TOP-Y**
1 : 50

05-MESH-TOP-Y Schedule							
S_PARTION	Bar Diameter	Mark	Bar Length	Quantity	Total Bar Length	METRIC WEIGHT	WEIGHT
MESH-TOP-Y	10 mm	21	8840 mm	3	26520 mm	0.617284	0.01637
MESH-TOP-Y	10 mm	28	7440 mm	2	14880 mm	0.617284	0.009185
MESH-TOP-Y	10 mm	37	1230 mm	1	1230 mm	0.617284	0.000759
MESH-TOP-Y	10 mm	39	4070 mm	2	8140 mm	0.617284	0.005025
MESH-TOP-Y	10 mm	40	6580 mm	14	92120 mm	0.617284	0.056864
MESH-TOP-Y	10 mm	42	7860 mm	12	94320 mm	0.617284	0.058222
MESH-TOP-Y	10 mm	43	5010 mm	12	60120 mm	0.617284	0.037111
MESH-TOP-Y	10 mm	46	3080 mm	15	46200 mm	0.617284	0.028519
MESH-TOP-Y	10 mm	47	2770 mm	3	8310 mm	0.617284	0.00513
MESH-TOP-Y	10 mm	49	3560 mm	12	42720 mm	0.617284	0.02637
MESH-TOP-Y	10 mm	50	1880 mm	1	1880 mm	0.617284	0.00116
MESH-TOP-Y	10 mm	51	10410 mm	1	10410 mm	0.617284	0.006426
MESH-TOP-Y	10 mm	52	5630 mm	8	45040 mm	0.617284	0.027802
MESH-TOP-Y	10 mm	53	4050 mm	10	40500 mm	0.617284	0.025
MESH-TOP-Y	10 mm	54	6510 mm	2	13020 mm	0.617284	0.008037
MESH-TOP-Y	10 mm	55	2320 mm	12	27840 mm	0.617284	0.017185
MESH-TOP-Y	10 mm	56	4880 mm	15	73200 mm	0.617284	0.045185
MESH-TOP-Y	10 mm	57	1920 mm	4	7680 mm	0.617284	0.004741
MESH-TOP-Y	10 mm	58	1680 mm	4	6720 mm	0.617284	0.004148
MESH-TOP-Y	10 mm	59	8150 mm	10	81500 mm	0.617284	0.050309
MESH-TOP-Y	10 mm	62	5850 mm	11	64350 mm	0.617284	0.039722
MESH-TOP-Y	10 mm	101	5450 mm	11	59950 mm	0.617284	0.037006
MESH-TOP-Y	10 mm	101	5450 mm	23	125350 mm	0.617284	0.077377
MESH-TOP-Y	10 mm	105	4450 mm	21	93450 mm	0.617284	0.057685
MESH-TOP-Y	10 mm	106	10960 mm	21	230160 mm	0.617284	0.142074
MESH-TOP-Y	10 mm	107	9730 mm	3	29190 mm	0.617284	0.018019
MESH-TOP-Y	10 mm	108	4560 mm	20	91200 mm	0.617284	0.056296
MESH-TOP-Y	10 mm	111	7750 mm	6	46500 mm	0.617284	0.028704
MESH-TOP-Y	10 mm	113	3150 mm	11	34650 mm	0.617284	0.021389
					1477150 mm		0.911821

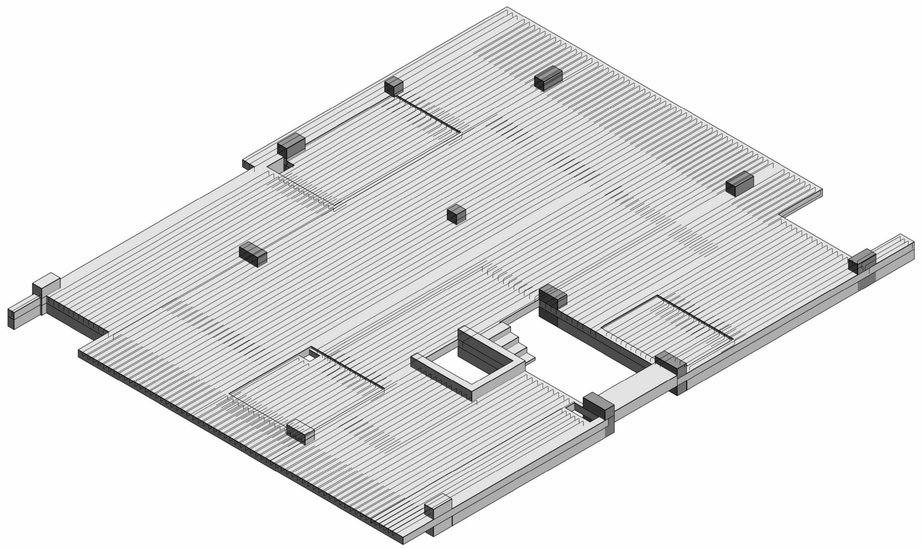


2 **RFT-MESH-TOP Y**

CONSULTANT

CONTRACTOR

NOTES

KEY PLAN

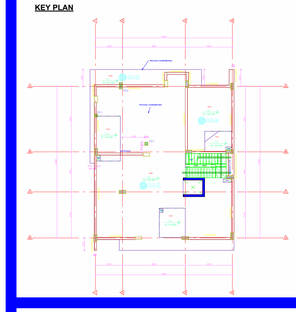

REVISION SCHEDULE

REV	Date	ISSUED FOR	Issued by	Issued to

DISCIPLINE

SHEET TILLE

RFT-MESH-TOP-Y


DRW BY : KHALED ATEF

CHK BY : Checker

SCALE

1 : 50

REVISION

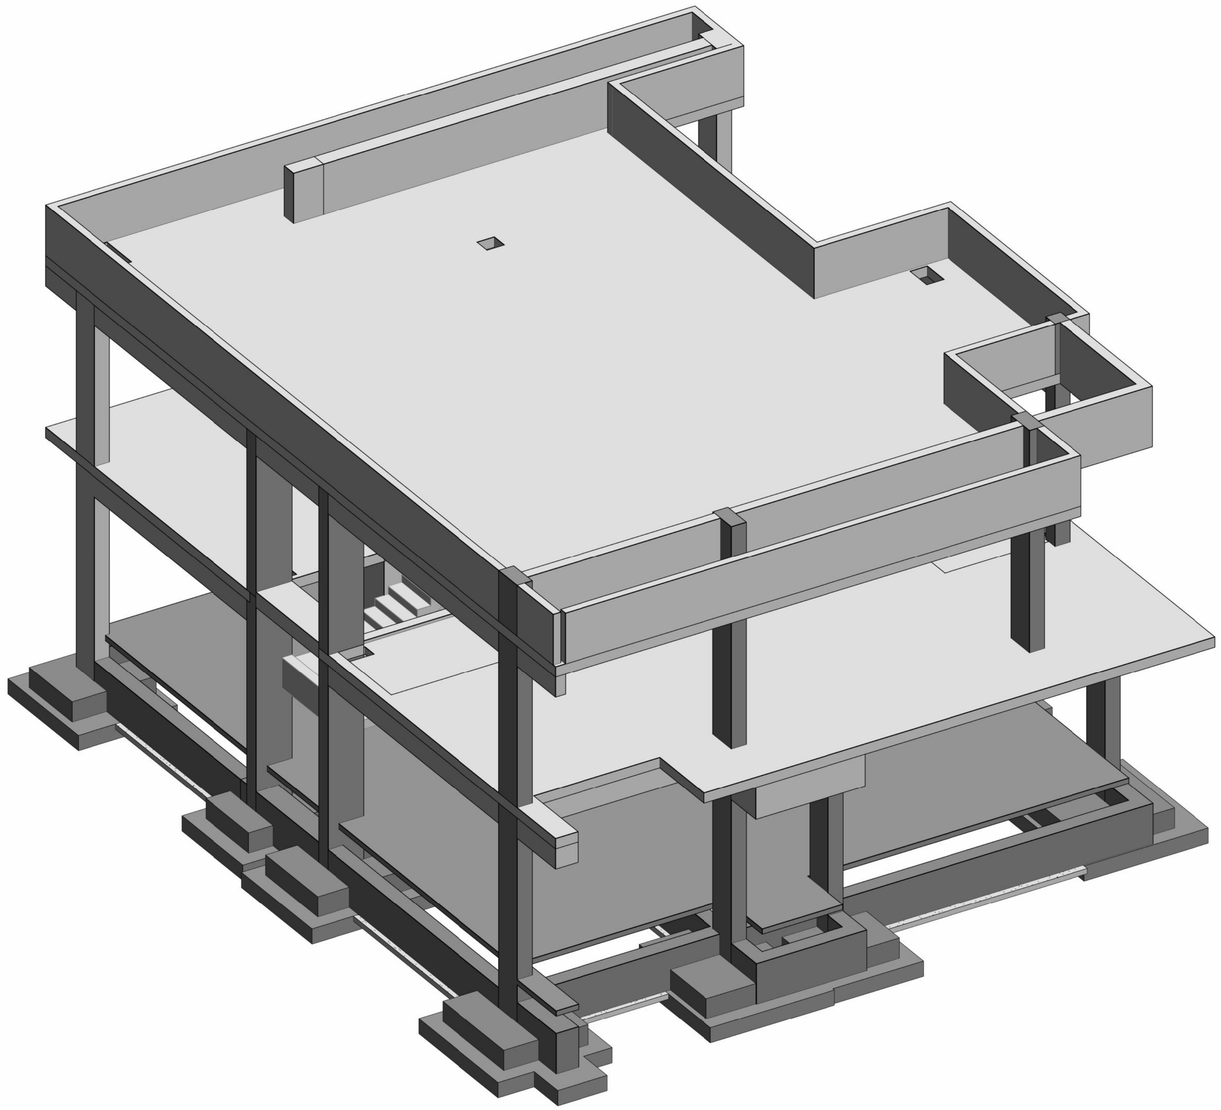

1 **3D SHOT**


Sheet List	
Sheet Name	Sheet Number
RFT-MESH-BOT-X	A100
RFT-MESH-TOP-Y	A101
BEAMS KEY PLANE	A102
BEAMS RFT SECTIONS	A103
FOUNDATIONS KEYPLAN	A105
FOUNDATION RFT DETAILING SECTIONS(F1-F2))	A106
FOUNDATION RFT DETAILING SECTIONS (F3-F4)	A107
TIE BEAMS KEYPLAN& TB1 SEC	A108
1 ST COULMNS_KEYPLAN	A109
1 ST COULMNS_KEYPLAN SECTIONS	A110
STAIR KEYPLAN & SECTIONS	A111
Q.S FOR CONCRETE	A112

CONSULTANT

CONTRACTOR

NOTES

KEY PLAN

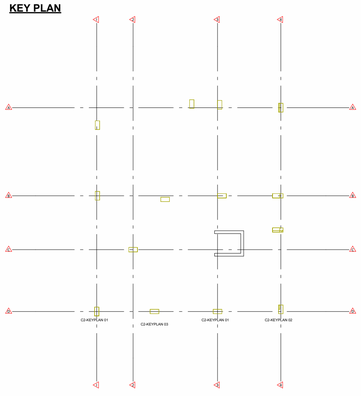

REVISION SCHEDULE

REV	Date	ISSUED FOR	Issued by	Issued to

DISCIPLINE

SHEET TILLE

INITIAL VIEW

DRW BY :


KHALED ATEF

CHK BY :


Checker


SCALE


REVISION

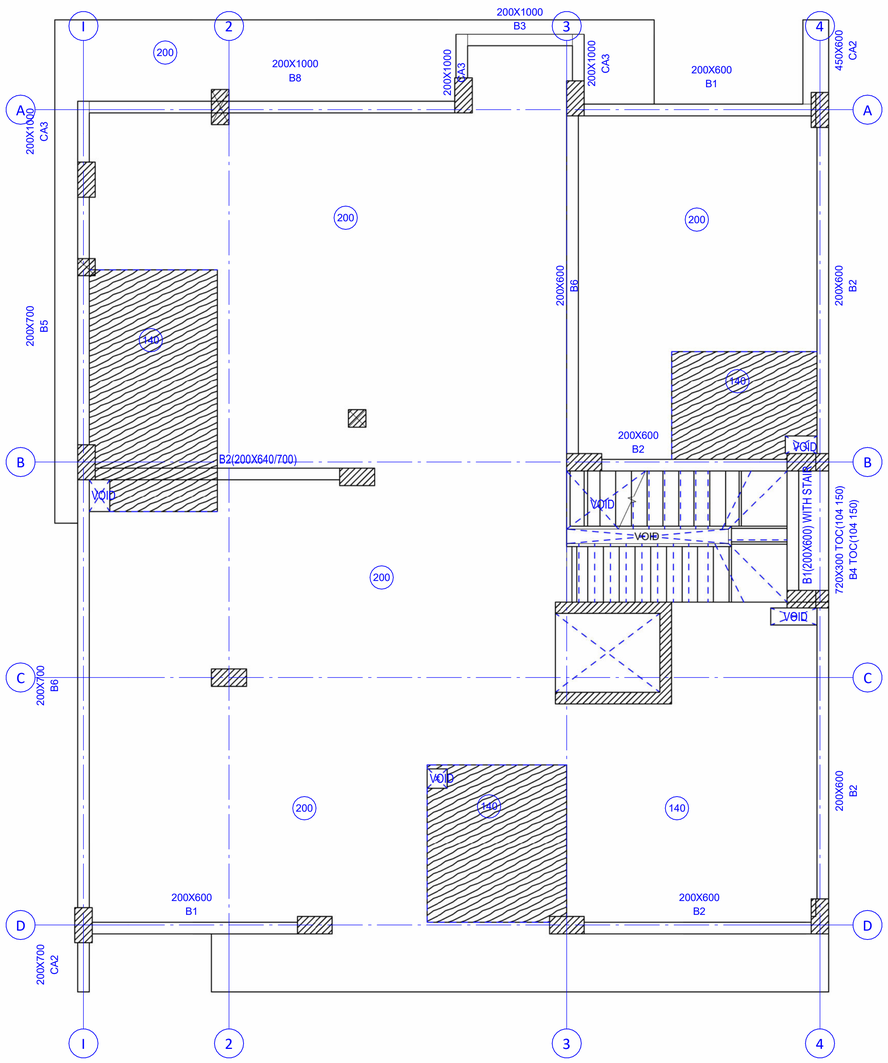

1 **BEAMS KEY PLAN**
1 : 50

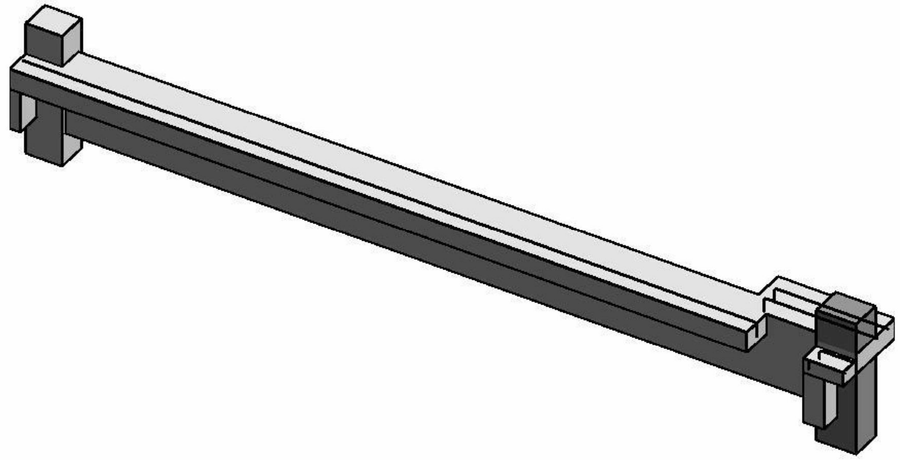

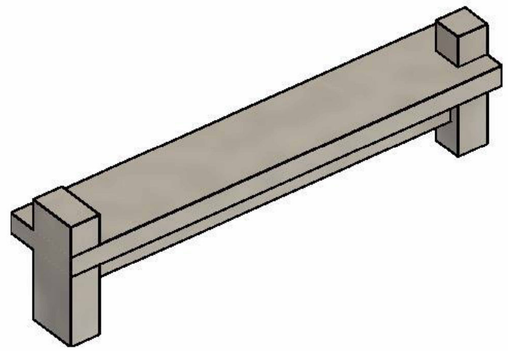

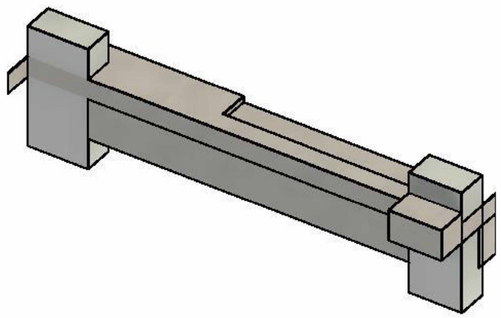


CONSULTANT

CONTRACTOR

NOTES

KEY PLAN

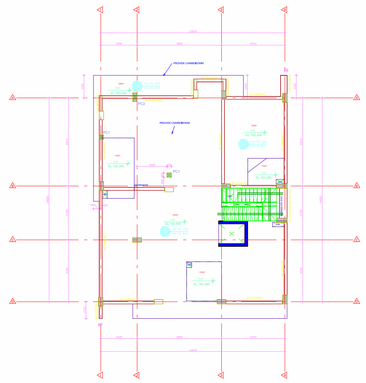

REVISION SCHEDULE

REV	Date	ISSUED FOR	Issued by	Issued to

DISCIPLINE

SHEET TILLE

BEAMS KEY PLANE

DRW BY :

KHALED ATEF


CHK BY :

Checker


SCALE

1 : 50


REVISION

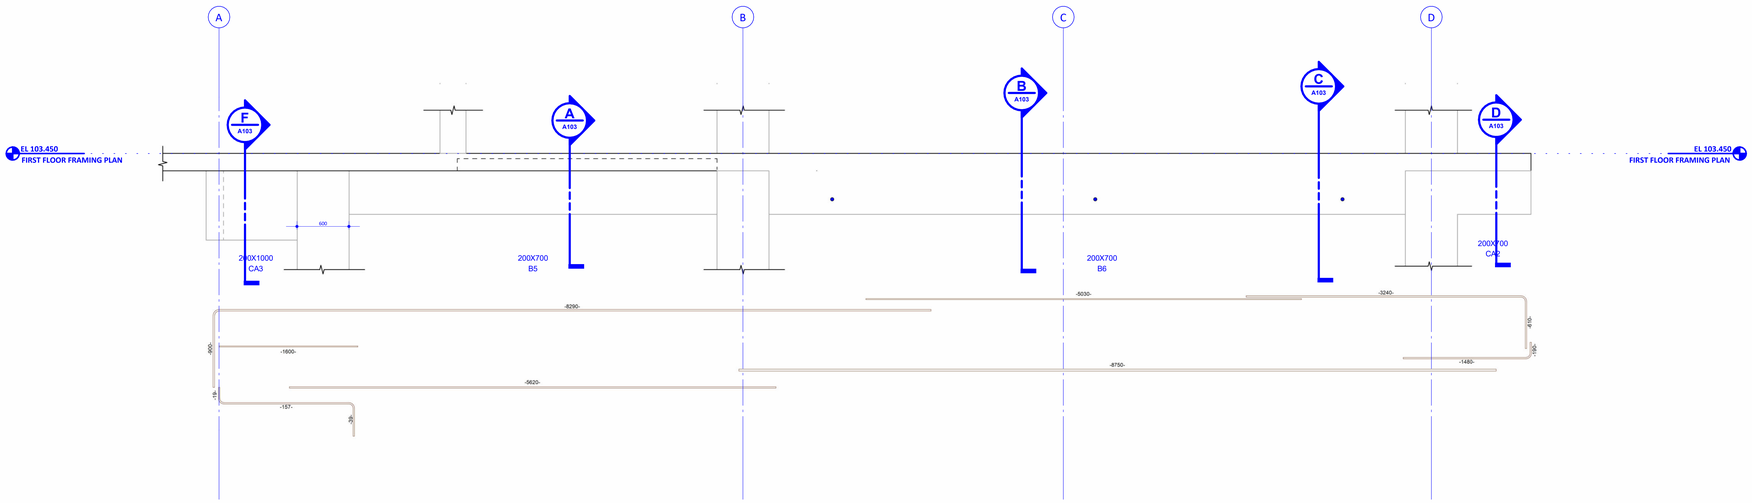


01 BEAM DETAIL 01
1 : 25

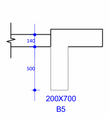


A SEC A-A
1 : 25

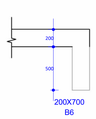

C SEC C-C
1 : 25

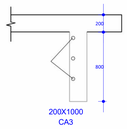

F SEC F-F
1 : 25

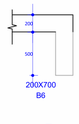

B SEC B-B
1 : 25



D SEC D-D
1 : 25

01-BEAMS Schedule								
S_PARTION	Bar Diameter	Mark	Bar Length	Quantity	Total Bar Length	METRIC WEIGHT	WEIGHT	Image
BEAMS	8 mm	115	1550 mm	11	17050 mm	0.395062	0.006736	
BEAMS	12 mm	116	3620 mm	4	14480 mm	0.888889	0.012871	
BEAMS	12 mm	116	3620 mm	4	14480 mm	0.888889	0.012871	


CONSULTANT

KAITECH
ENGINEERING AND TECHNOLOGY

CONTRACTOR

NOTES

KEY PLAN

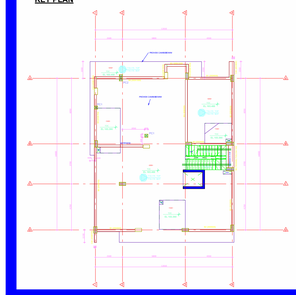

REVISION SCHEDULE

REV	Date	ISSUED FOR	Issued by	Issued to

DISCIPLINE

SHEET TILLE

BEAMS RFT SECTIONS


DRW BY : KHALED ATEF

CHK BY : KAITECH


SCALE

1 : 25

REVISION

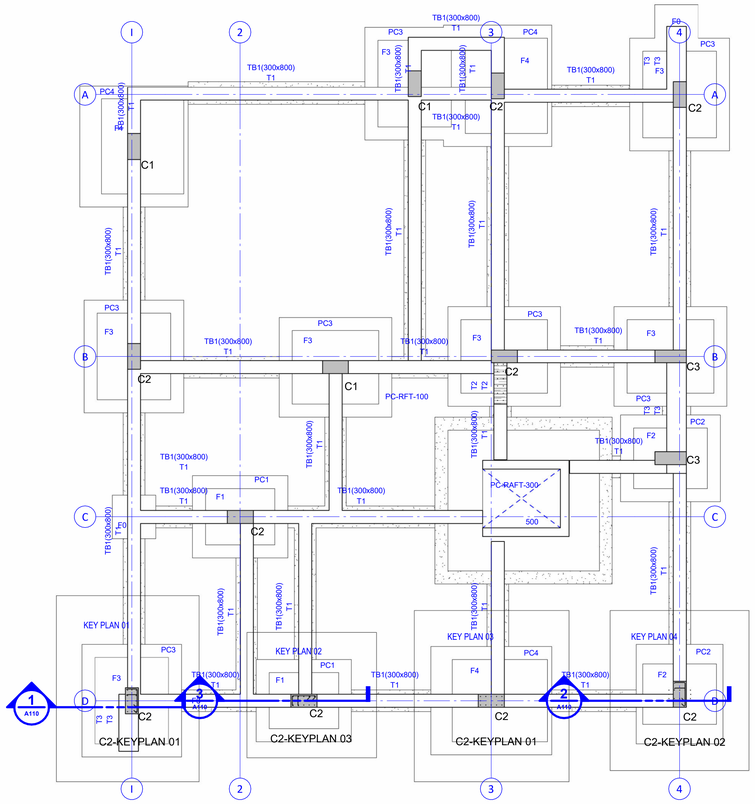

1 **FOUNDATION KEYPLAN**
1 : 50

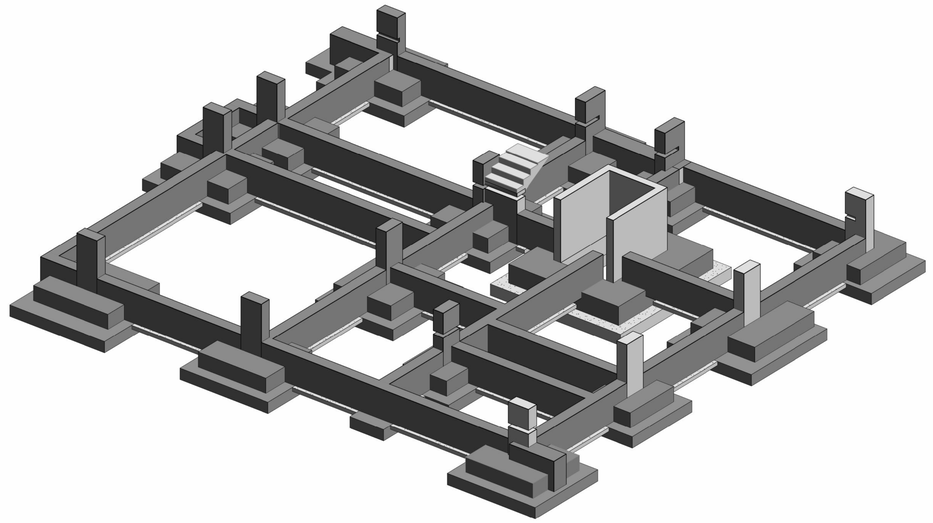

2 **FOUNDATION 3D**


CONSULTANT

KAITECH
ENGINEERING AND TECHNOLOGY

CONTRACTOR

NOTES

KEY PLAN

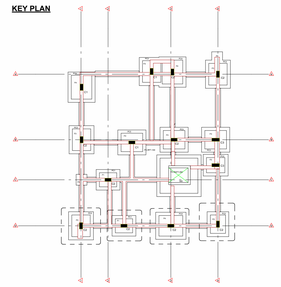

REVISION SCHEDULE

REV	Date	ISSUED FOR	Issued by	Issued to

DISCIPLINE

SHEET TILLE

FOUNDATIONS KEYPLAN


DRW BY : KHALED ATEF

CHK BY : KAITECH


SCALE

1 : 50

REVISION

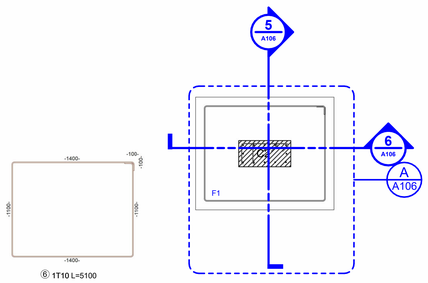


1 F1-C2 KEYPLAN
1 : 25

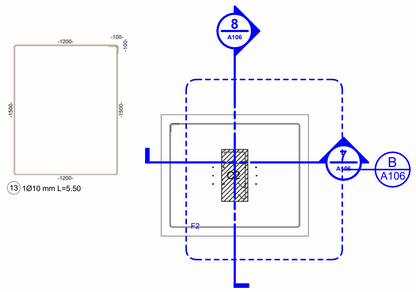


2 F2-C2 KEYPLAN
1 : 25


03-FOOTING Schedule								
S_PARTION	Bar Diameter	Mark	Bar Length	Quantity	Total Bar Length	METRIC WEIGHT	WEIGHT	Image
FOOTING	12 mm	1	1890 mm	7	13230 mm	0.888889	0.01176	
FOOTING	12 mm	2	1570 mm	8	12560 mm	0.888889	0.011164	
FOOTING	8 mm	3	1680 mm	6	10080 mm	0.395062	0.003982	
FOOTING	8 mm	5	1160 mm	6	6960 mm	0.395062	0.00275	
FOOTING	10 mm	6	5100 mm	1	5100 mm	0.617284	0.003148	
FOOTING	12 mm	8	2010 mm	8	16080 mm	0.888889	0.014293	
FOOTING	12 mm	9	1670 mm	9	15030 mm	0.888889	0.01336	
FOOTING	10 mm	13	5500 mm	1	5500 mm	0.617284	0.003395	

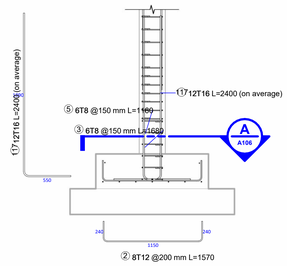


5 F1-C2-SEC01
1 : 25

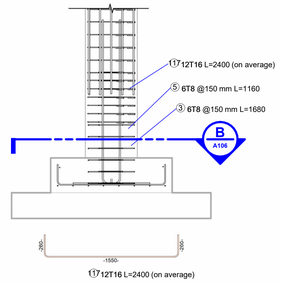


8 F2_C2-SEC01
1 : 25

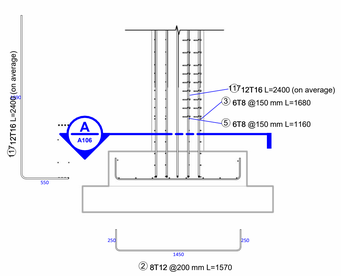


6 F1-C2-SEC02
1 : 25

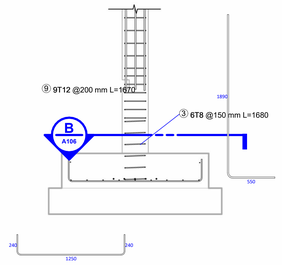

7 F2-C2-SEC02
1 : 25

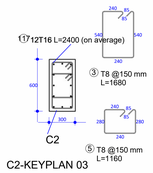

A C2-CROSS SEC
1 : 25

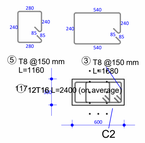

B C2-CROSS SEC1
1 : 25


CONSULTANT

KAITECH
ENGINEERING AND TECHNOLOGY

CONTRACTOR

NOTES

KEY PLAN

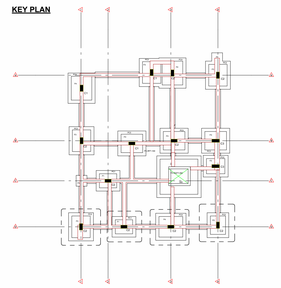

REVISION SCHEDULE

REV	Date	ISSUED FOR	Issued by	Issued to

DISCIPLINE

SHEET TILLE

FOUNDATION RFT DETAILING SECTIONS(F1-F2))


DRW BY : KHALED ATEF

CHK BY : Checker


SCALE

1 : 25


REVISION

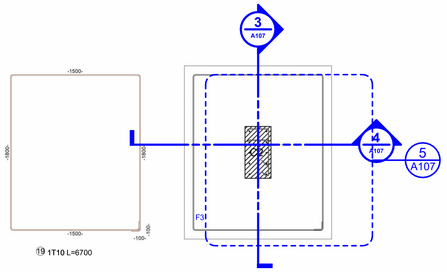


1 F3-C2 KEYPLAN
1 : 25

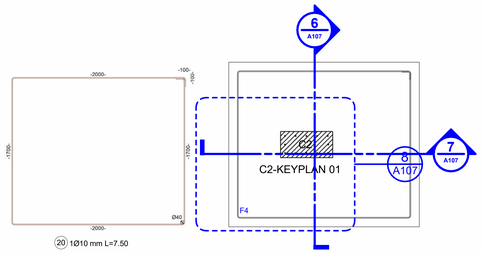

2 F4-C2 KEYPLAN
1 : 25

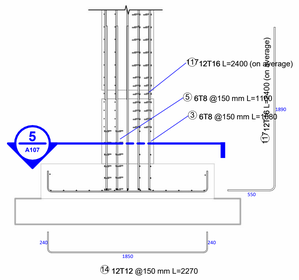


3 F3-C2-SEC01
1 : 25

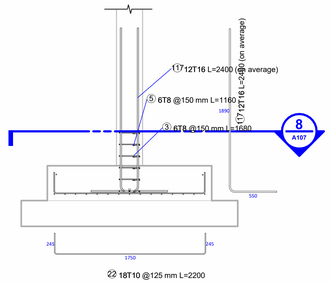


6 F4-C2-SEC01
1 : 25


03-FOOTING Schedule								
S_PARTION	Bar Diameter	Mark	Bar Length	Quantity	Total Bar Length	METRIC WEIGHT	WEIGHT	Image
FOOTING	12 mm	14	2270 mm	12	27240 mm	0.888889	0.024213	
FOOTING	12 mm	15	1970 mm	13	25610 mm	0.888889	0.022764	
FOOTING	10 mm	19	6700 mm	1	6700 mm	0.617284	0.004136	
FOOTING	10 mm	20	7500 mm	1	7500 mm	0.617284	0.00463	
FOOTING	10 mm	21	2520 mm	15	37800 mm	0.617284	0.023333	
FOOTING	10 mm	22	2200 mm	18	39600 mm	0.617284	0.024444	
FOOTING	16 mm	117	2400 mm	12	28800 mm	1.580247	0.045511	

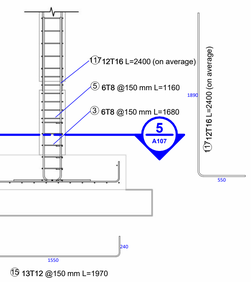


4 F3-C2-SEC02
1 : 25

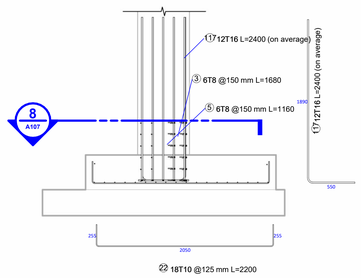

7 F4-C2-SEC02
1 : 25

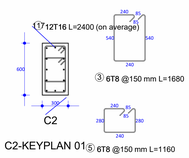

5 C2-CROSS SEC2
1 : 25

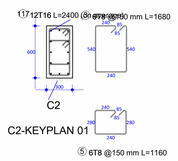

8 C2-CROSS SEC3
1 : 25


CONSULTANT

KAITECH
ENGINEERING AND TECHNOLOGY

CONTRACTOR

NOTES

KEY PLAN

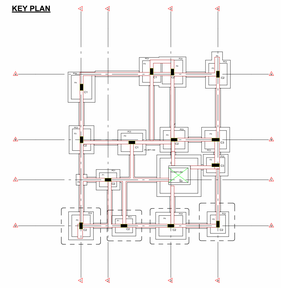

REVISION SCHEDULE

REV	Date	ISSUED FOR	Issued by	Issued to

DISCIPLINE

SHEET TILLE

FOUNDATION RFT DETAILING SECTIONS (F3-F4)


DRW BY : KHALED ATEF

CHK BY : KAITECH


SCALE

1 : 25


REVISION

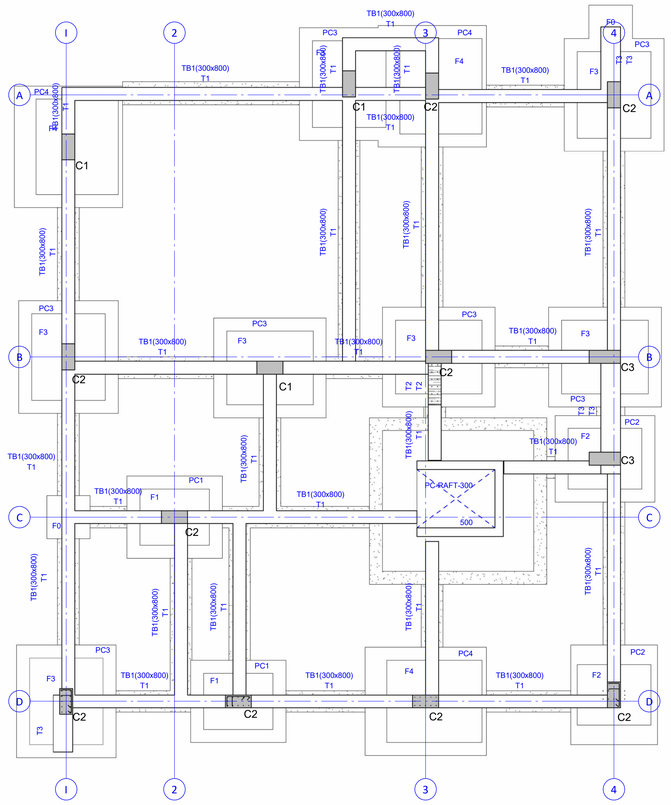

1 TIE BEAMS KEYPLAN
1 : 50

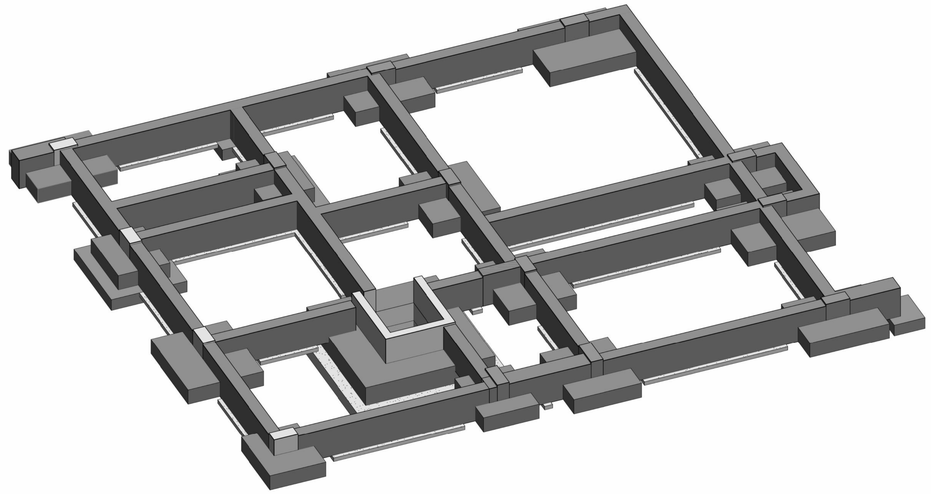

4 TIE BEAMS 3D

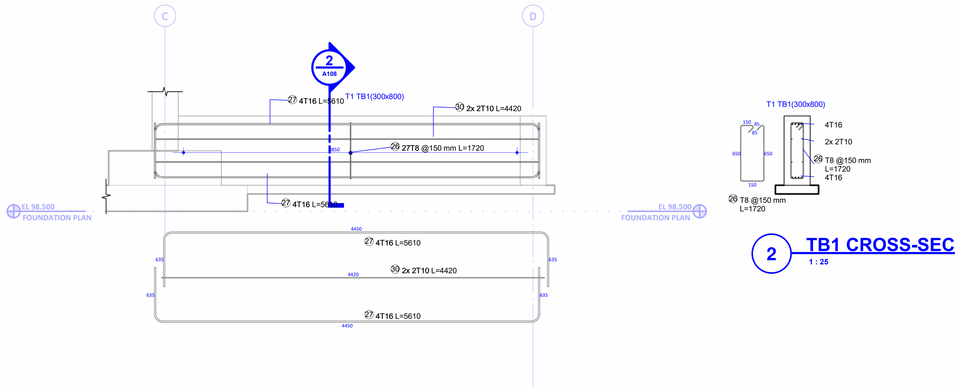

3 TB1 SEC
1 : 25

2 TB1 CROSS-SEC
1 : 25

07-TIE BEAMS Schedule								
S_PARTION	Bar Diameter	Mark	Bar Length	Quantity	Total Bar Length	METRIC WEIGHT	WEIGHT	Image
TIE BEAMS	8 mm	26	1720 mm	27	46440 mm	0.395062	0.018347	
TIE BEAMS	16 mm	27	5610 mm	4	22440 mm	1.580247	0.035461	
TIE BEAMS	10 mm	30	4420 mm	2	8840 mm	0.617284	0.005457	


CONSULTANT

KAITECH
ENGINEERING AND TECHNOLOGY

CONTRACTOR

NOTES

KEY PLAN

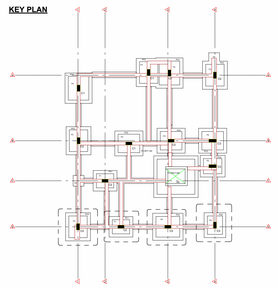

REVISION SCHEDULE

REV	Date	ISSUED FOR	Issued by	Issued to

DISCIPLINE

SHEET TILLE

TIE BEAMS KEYPLAN& TB1 SEC


DRW BY : KHALED ATEF

CHK BY : KAITECH

SCALE


As indicated

REVISION

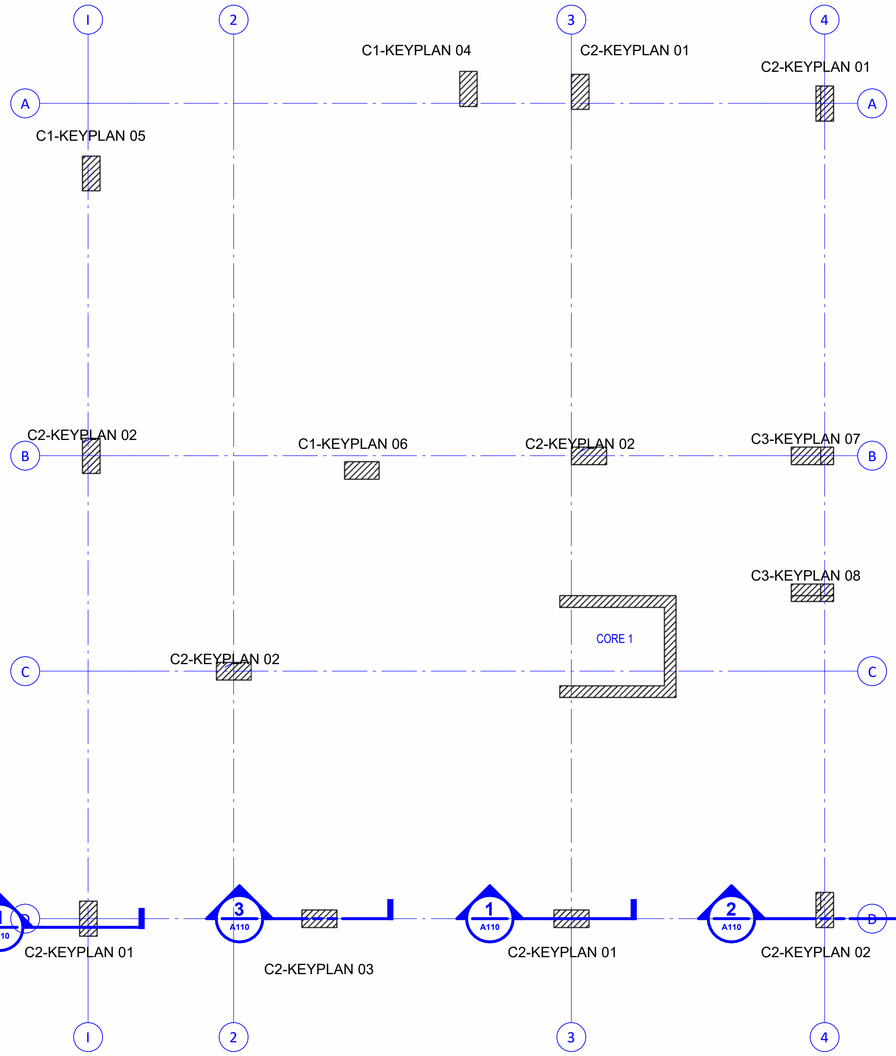

1 1ST COULMNS_KEYPLAN

1 : 50

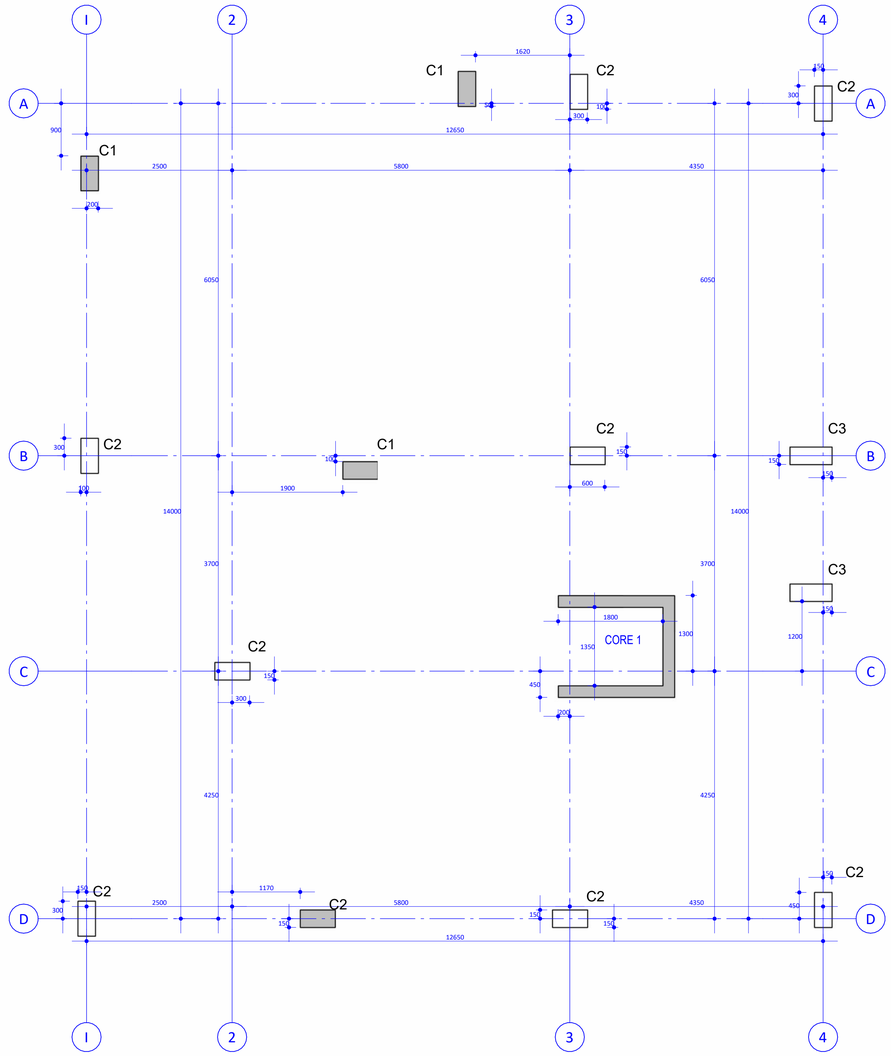

2 COLUMNS & AXES


1 : 50

CONSULTANT

CONTRACTOR

NOTES

KEY PLAN

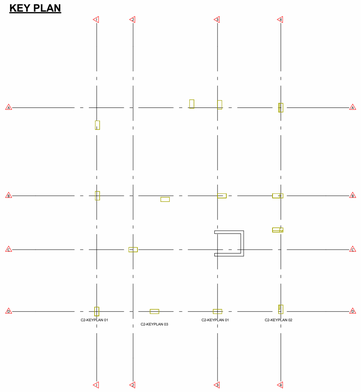

REVISION SCHEDULE

REV	Date	ISSUED FOR	Issued by	Issued to

DISCIPLINE

SHEET TILLE

1 ST COULMNS_KEYPLAN

DRW BY :

KHALED ATEF


CHK BY :

Checker

SCALE

1 : 50


REVISION

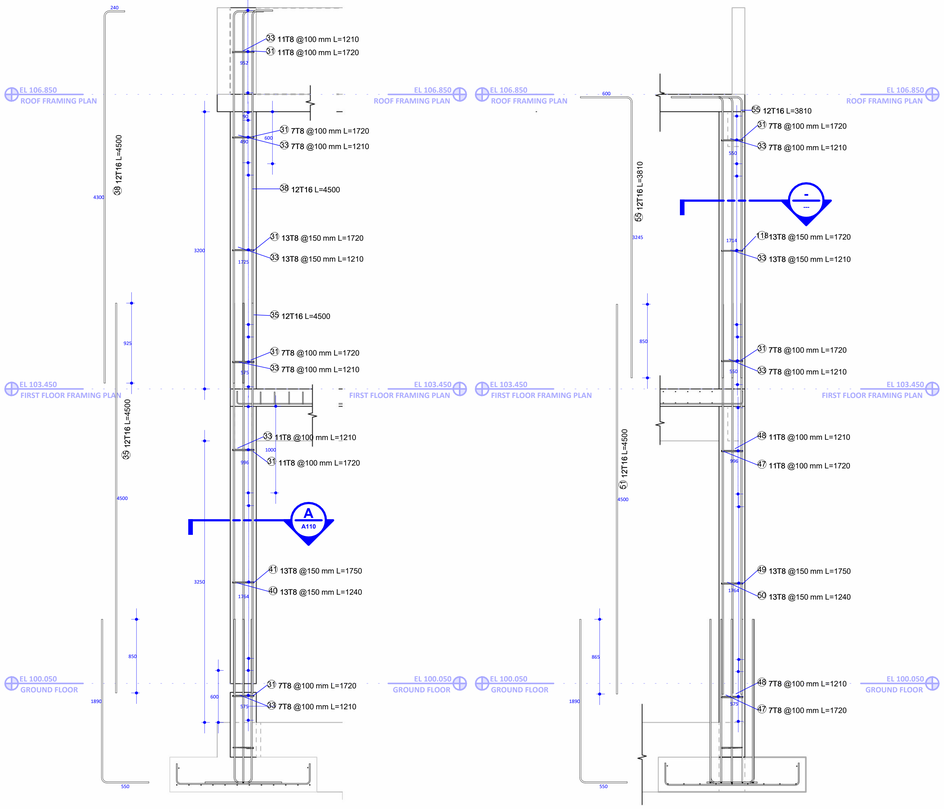


1 **C2-KEYPLAN 01**
1 : 25

2 **C2-KEYPLAN 02**
1 : 25

3 **C2-KEYPLAN 03**
1 : 25

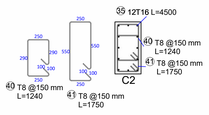

A **C2-KEYPLAN 01-CROSS SEC**
1 : 25

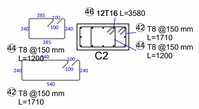

C **C2-KEYPLAN 03-CROSS SEC**
1 : 25

02-COULMNS Schedule								
S_PARTION	Bar Diameter	Mark	Bar Length	Quantity	Total Bar Length	METRIC WEIGHT	WEIGHT	Image
COULMNS	8 mm	31	1720 mm	7	60200 mm	0.395062	0.023783	
COULMNS	8 mm	31	1720 mm	11	37840 mm	0.395062	0.014949	
COULMNS	8 mm	31	1720 mm	13	22360 mm	0.395062	0.008834	
COULMNS	8 mm	33	1210 mm	7	42350 mm	0.395062	0.016731	
COULMNS	8 mm	33	1210 mm	11	26620 mm	0.395062	0.010517	
COULMNS	8 mm	33	1210 mm	13	31460 mm	0.395062	0.012429	
COULMNS	16 mm	35	4500 mm	12	54000 mm	1.580247	0.085333	
COULMNS	16 mm	38	4500 mm	12	54000 mm	1.580247	0.085333	
COULMNS	8 mm	40	1240 mm	13	16120 mm	0.395062	0.006368	
COULMNS	8 mm	41	1750 mm	13	22750 mm	0.395062	0.008988	
COULMNS	8 mm	42	1710 mm	7	11970 mm	0.395062	0.004729	
COULMNS	8 mm	42	1710 mm	11	18810 mm	0.395062	0.007431	
COULMNS	8 mm	42	1710 mm	13	22230 mm	0.395062	0.008782	
COULMNS	8 mm	44	1200 mm	7	8400 mm	0.395062	0.003319	
COULMNS	8 mm	44	1200 mm	11	13200 mm	0.395062	0.005215	
COULMNS	8 mm	44	1200 mm	13	15600 mm	0.395062	0.006163	
COULMNS	16 mm	46	3580 mm	12	42910 mm	1.580247	0.067808	
COULMNS	8 mm	47	1720 mm	7	12040 mm	0.395062	0.004757	
COULMNS	8 mm	47	1720 mm	11	18920 mm	0.395062	0.007475	
COULMNS	8 mm	48	1210 mm	7	8470 mm	0.395062	0.003346	
COULMNS	8 mm	48	1210 mm	11	13310 mm	0.395062	0.005258	
COULMNS	8 mm	49	1750 mm	13	22750 mm	0.395062	0.008988	
COULMNS	8 mm	50	1240 mm	13	16120 mm	0.395062	0.006368	
COULMNS	16 mm	51	4500 mm	12	54000 mm	1.580247	0.085333	
COULMNS	16 mm	55	3810 mm	12	45690 mm	1.580247	0.072201	
COULMNS	8 mm	118	1720 mm	13	22360 mm	0.395062	0.008834	
					714480 mm		0.579271	


CONSULTANT

KAITECH
ENGINEERING AND TECHNOLOGY

CONTRACTOR

NOTES

KEY PLAN

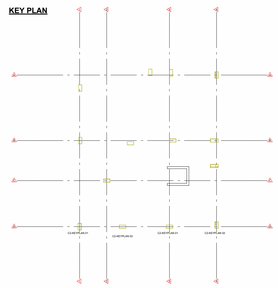

REVISION SCHEDULE

REV	Date	ISSUED FOR	Issued by	Issued to

DISCIPLINE

SHEET TILLE

1 ST COULMNS_KEYPLAN SECTIONS


DRW BY : KHALED ATEF

CHK BY : KAITECH


SCALE

1 : 25

REVISION

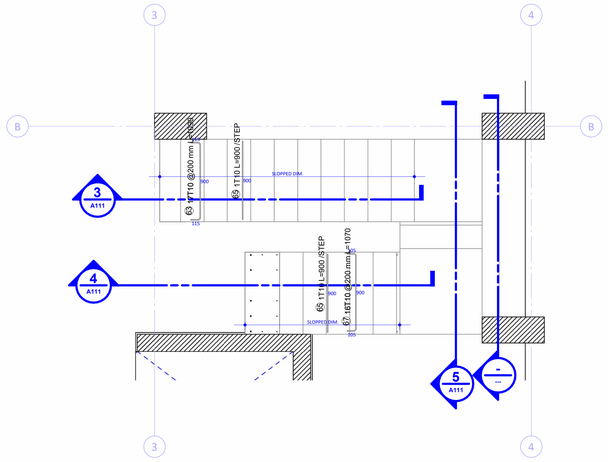


1 **STAIR**
1 : 25

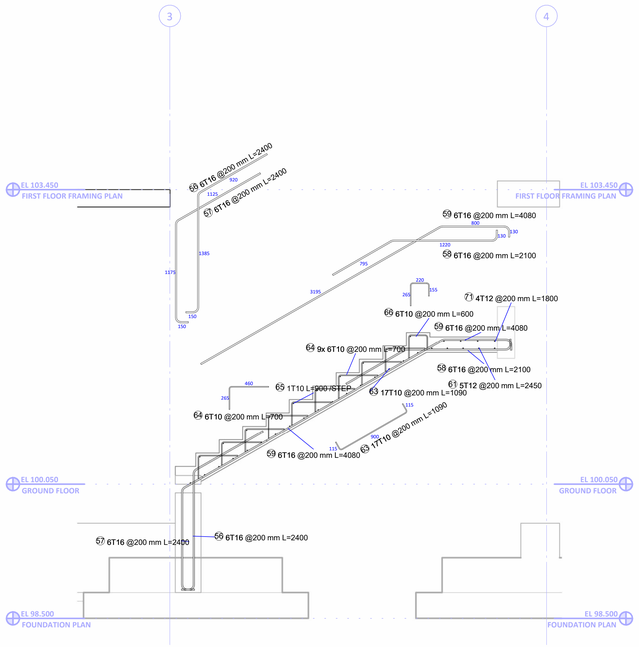


3 **STAIR_SEC 1**
1 : 25


06-STAIRS Schedule								
S_PARTION	Bar Diameter	Mark	Bar Length	Quantity	Total Bar Length	METRIC WEIGHT	WEIGHT	Image
STAIRS	16 mm	56	2400 mm	6	14400 mm	1.580247	0.022756	
STAIRS	16 mm	57	2400 mm	6	14400 mm	1.580247	0.022756	
STAIRS	16 mm	58	2100 mm	6	12600 mm	1.580247	0.019911	
STAIRS	16 mm	59	4080 mm	6	24480 mm	1.580247	0.038684	
STAIRS	16 mm	60	5000 mm	6	30000 mm	1.580247	0.047407	
STAIRS	12 mm	61	2450 mm	5	12250 mm	0.888889	0.010889	
STAIRS	12 mm	62	1360 mm	6	8160 mm	0.888889	0.007253	
STAIRS	10 mm	63	1090 mm	17	18530 mm	0.617284	0.011438	
STAIRS	10 mm	64	700 mm	6	37800 mm	0.617284	0.023333	
STAIRS	10 mm	65	900 mm	1	18900 mm	0.617284	0.011667	
STAIRS	10 mm	66	600 mm	6	3600 mm	0.617284	0.002222	
STAIRS	10 mm	67	1070 mm	16	17120 mm	0.617284	0.010568	
STAIRS	10 mm	68	690 mm	6	37260 mm	0.617284	0.023	
STAIRS	10 mm	69	580 mm	6	3480 mm	0.617284	0.002148	
STAIRS	10 mm	70	530 mm	6	3180 mm	0.617284	0.001963	
STAIRS	12 mm	71	1800 mm	4	7200 mm	0.888889	0.0064	
STAIRS	12 mm	72	1730 mm	6	10380 mm	0.888889	0.009227	
					273740 mm		0.271622	

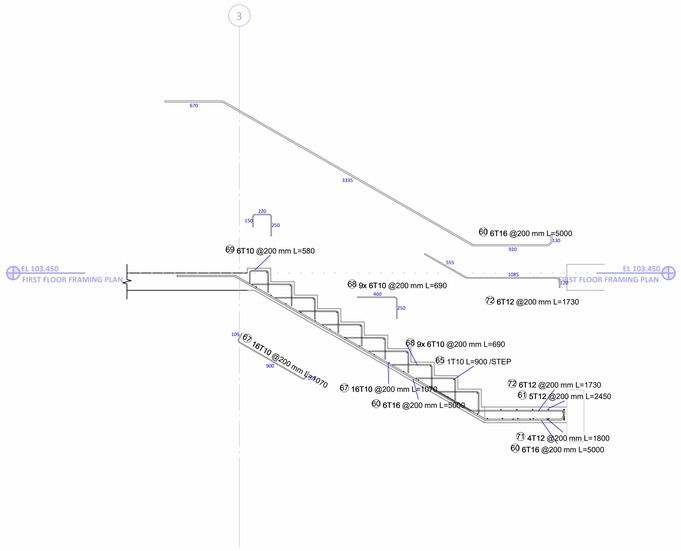


4 **STAIR_SEC 2**
1 : 25

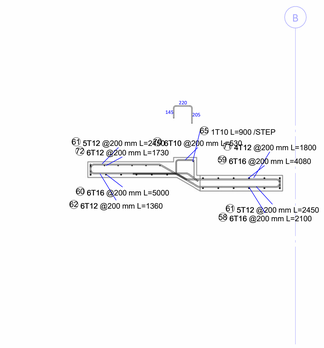

5 **STAIR_SEC 3**
1 : 25

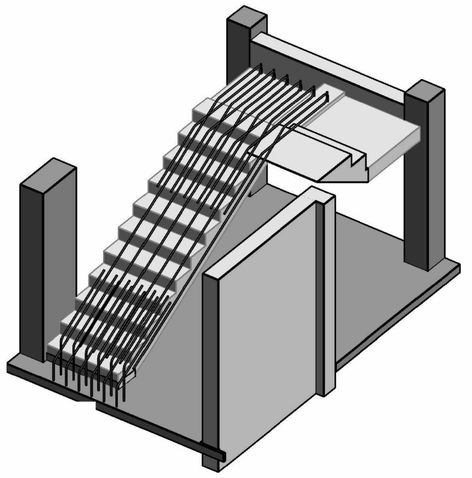

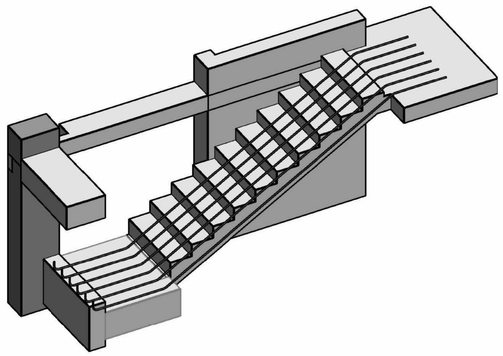



2 **STAIR BEAM -CROSS SEC**
1 : 25


CONSULTANT

KAITECH
ENGINEERING AND TECHNOLOGY

CONTRACTOR

NOTES

KEY PLAN

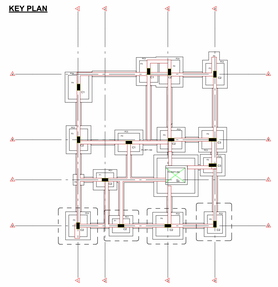

REVISION SCHEDULE

REV	Date	ISSUED FOR	Issued by	Issued to

DISCIPLINE

SHEET TILLE

STAIR KEYPLAN & SECTIONS

DRW BY : KHALED ATEF

CHK BY : KAITECH

SCALE

1 : 25

REVISION

Floor Schedule			
Level	Type	Core Thickness	Volume
GROUND FLOOR	Slab-RC-Ongrade -100	100	16.52 m³
FIRST FLOOR FRAMING PLAN	Slab-RC-Flat 140	140	2.75 m³
FIRST FLOOR FRAMING PLAN	Slab-RC-Flat 200	200	36.07 m³
ROOF FRAMING PLAN	Slab-RC-Flat 200	200	38.41 m³
			93.74 m³

Structural Framing Schedule				
Reference Level	Beam's type	Type	Count	Volume
FOUNDATION PLAN	TB1	T2	1	0.36 m³
FOUNDATION PLAN	TB1	T3	3	1.12 m³
FOUNDATION PLAN	TB1	TB1(300x800)	28	20.42 m³
FIRST FLOOR FRAMING PLAN	B0	200X600	8	2.71 m³
FIRST FLOOR FRAMING PLAN	B0	200X640	1	0.21 m³
FIRST FLOOR FRAMING PLAN	B0	200X700	4	1.45 m³
FIRST FLOOR FRAMING PLAN	B1	200X1000	5	1.71 m³
FIRST FLOOR FRAMING PLAN	B1	450X600	1	0.25 m³
FIRST FLOOR FRAMING PLAN	B0	720X300	1	0.44 m³
ROOF FRAMING PLAN	B0	200X600	7	1.48 m³
ROOF FRAMING PLAN	B0	200X1200	4	3.09 m³
ROOF FRAMING PLAN	T1	300X1200	1	2.36 m³
				35.61 m³

Structural Column Schedule			
Base Level	Column 's Type	Count	Volume
FOUNDATION PLAN	C1	3	2.19 m³
FOUNDATION PLAN	C2	9	6.50 m³
FOUNDATION PLAN	C3	2	1.75 m³
FIRST FLOOR FRAMING PLAN	C2	8	5.33 m³
FIRST FLOOR FRAMING PLAN	C3	2	1.38 m³
FIRST FLOOR FRAMING PLAN	PC1	2	0.67 m³
FIRST FLOOR FRAMING PLAN	PC2	1	0.76 m³
			18.57 m³


Structural Foundation Schedule		
FOOTING-KEYPLAN	Count	Volume
F0	2	0.53 m³
F1-C2	2	1.66 m³
F2-C2	1	0.95 m³
F2-C3	1	0.95 m³
F3-C1	2	2.72 m³
F3-C2	4	5.44 m³
F3-C3	1	1.36 m³
F4-C1	1	1.67 m³
F4-C2	2	3.34 m³
		18.64 m³

CONSULTANT

CONTRACTOR

NOTES

KEY PLAN

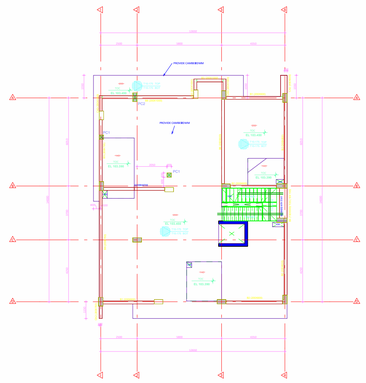

REVISION SCHEDULE

REV	Date	ISSUED FOR	Issued by	Issued to

DISCIPLINE

SHEET TILLE

Q.S FOR CONCRETE

DRW BY : KHALED ATEF

CHK BY : Checker

SCALE

REVISION